

План 1-го этажа

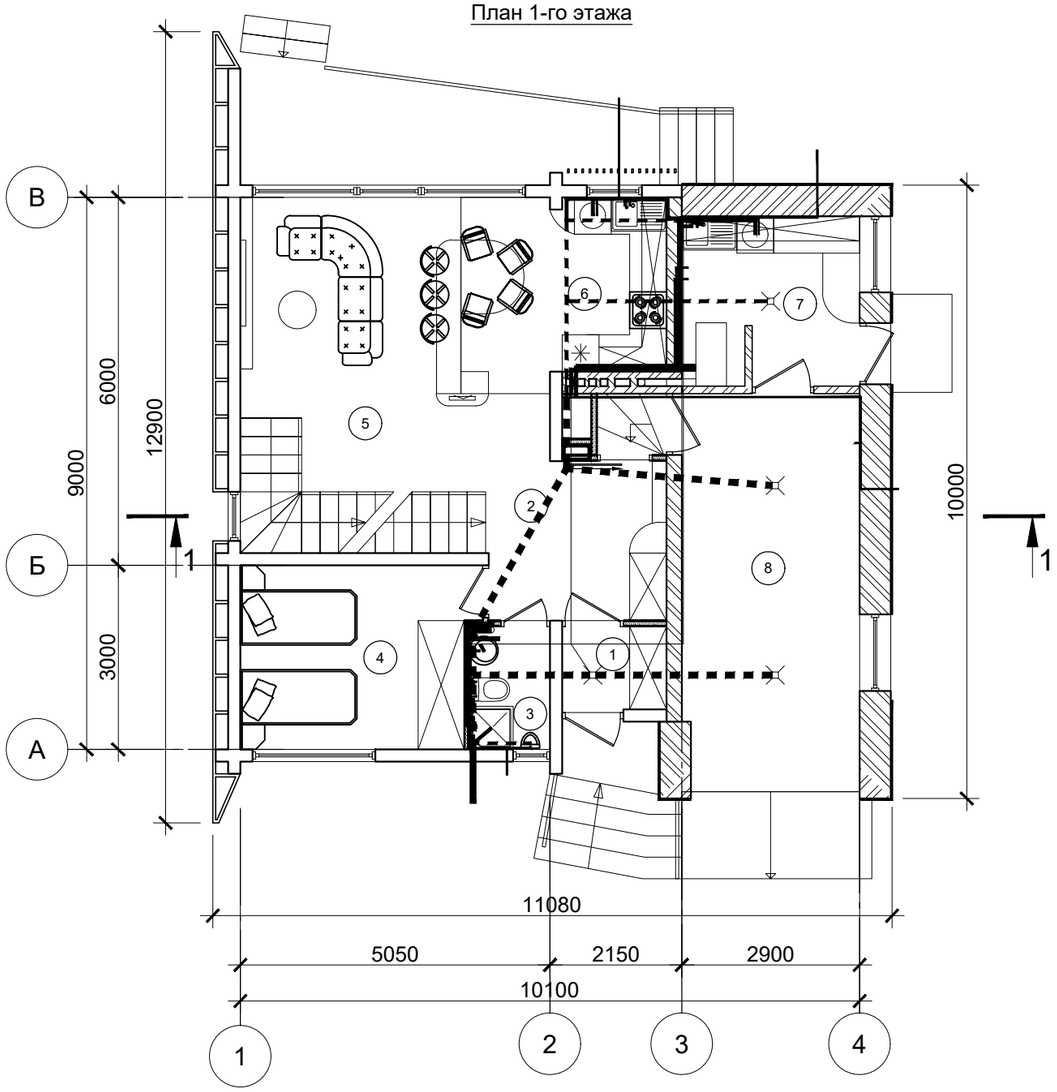

План мансардного этажа

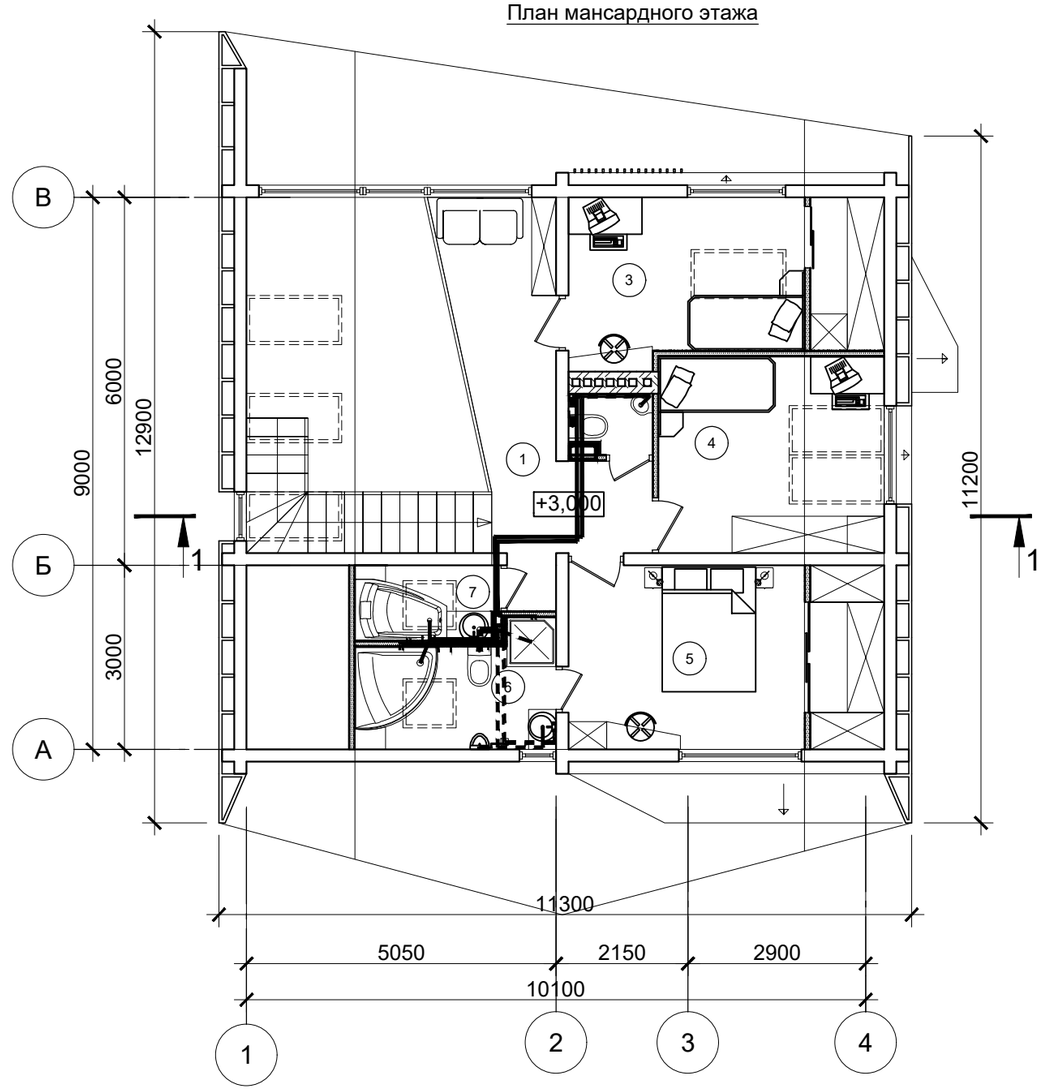

Экспликация помещений 1-го этажа

№ пом.	Наименование	Площадь м²	Кат. пом.
1	Тамбур	2,3	
2	Холл	7,3	
3	Санузел	2,6	
4	Спальня для гостей	11,2	
5	Гостиная	24,3	
6	Кухня-столовая	10,3	
7	Миникотельная	7,9	
8	Гараж	17,6	

Экспликация помещений мансардного этажа

№ пом.	Наименование	Площадь м²	Кат. пом.
1	Холл	11,6	
2	Туалет	1,3	
3	Спальня+гардеробная	13,3	
4	Спальня	11,8	
5	Спальня+гардеробная	15,5	
6	Санузел	5,9	
7	Ванная комната	2,9	

-ВК


Взам. инв. №

Подп. и дата

Инв. № подл

Копировал

А3

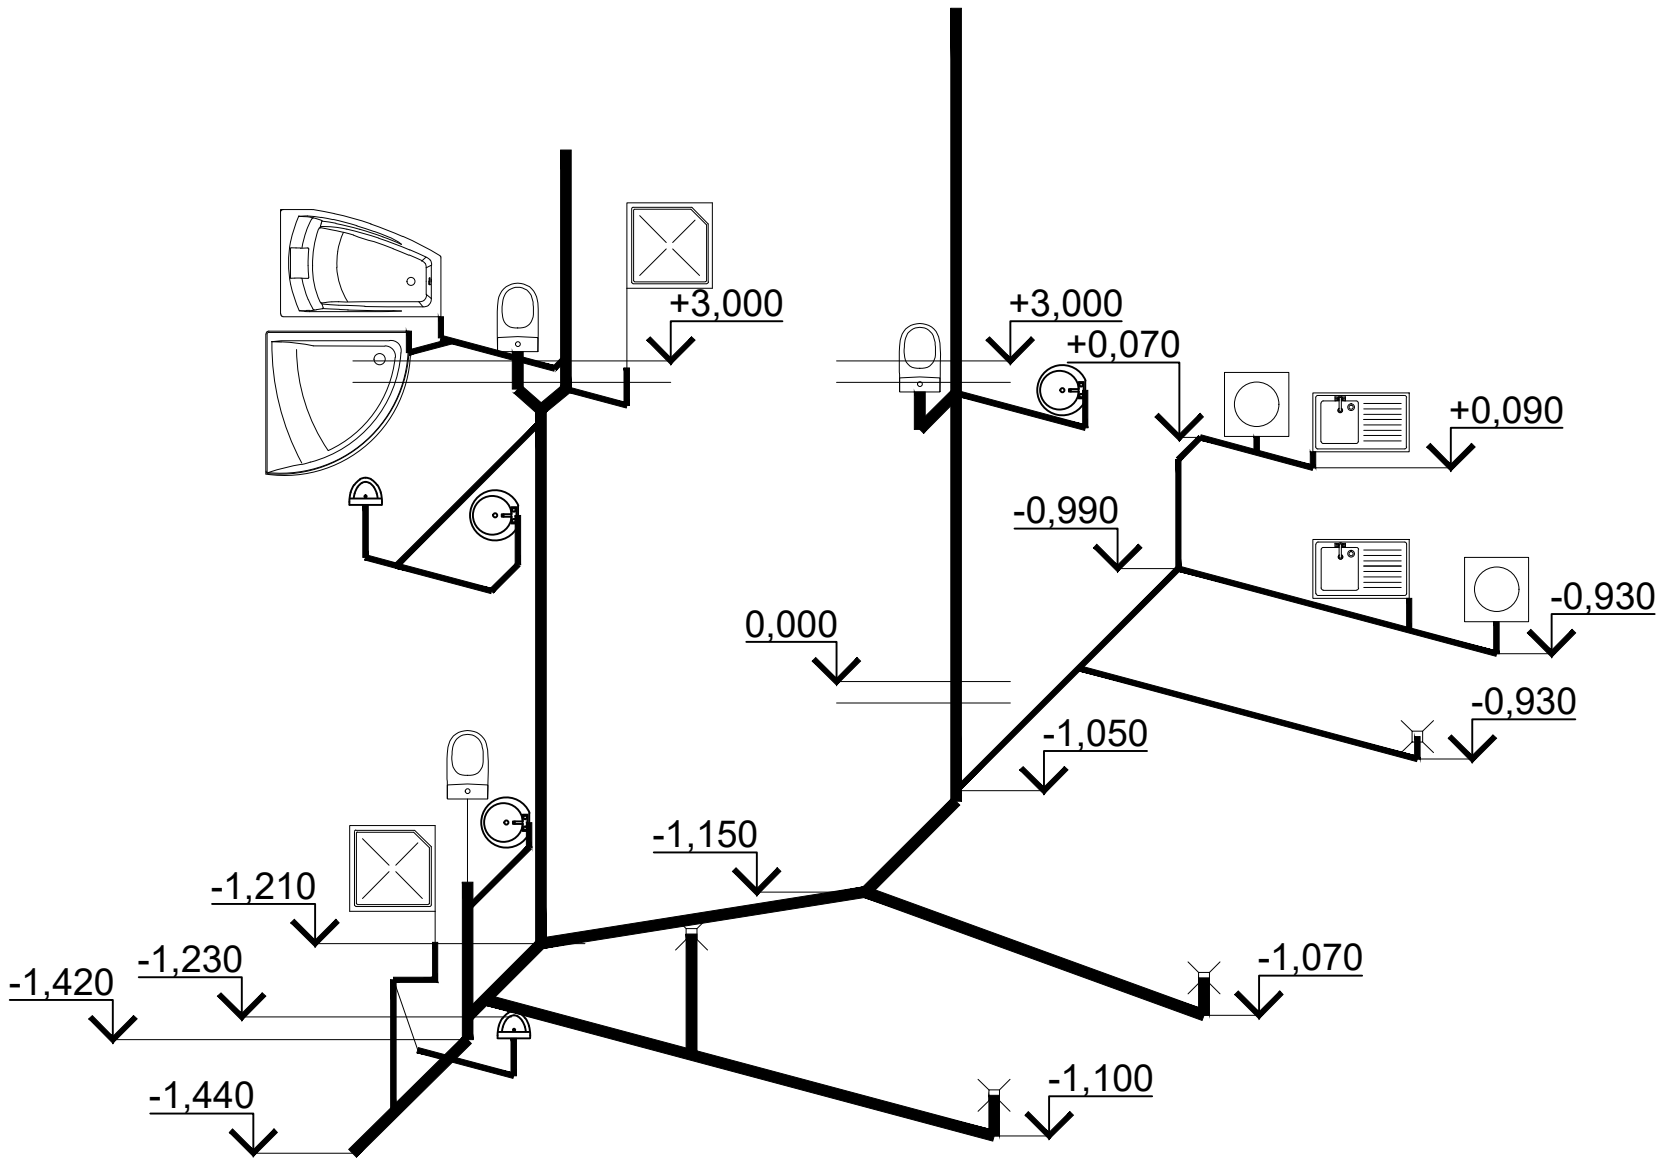

Инв. № подл. | Подп. и дата | Взам. инв. №

Копировал

А3