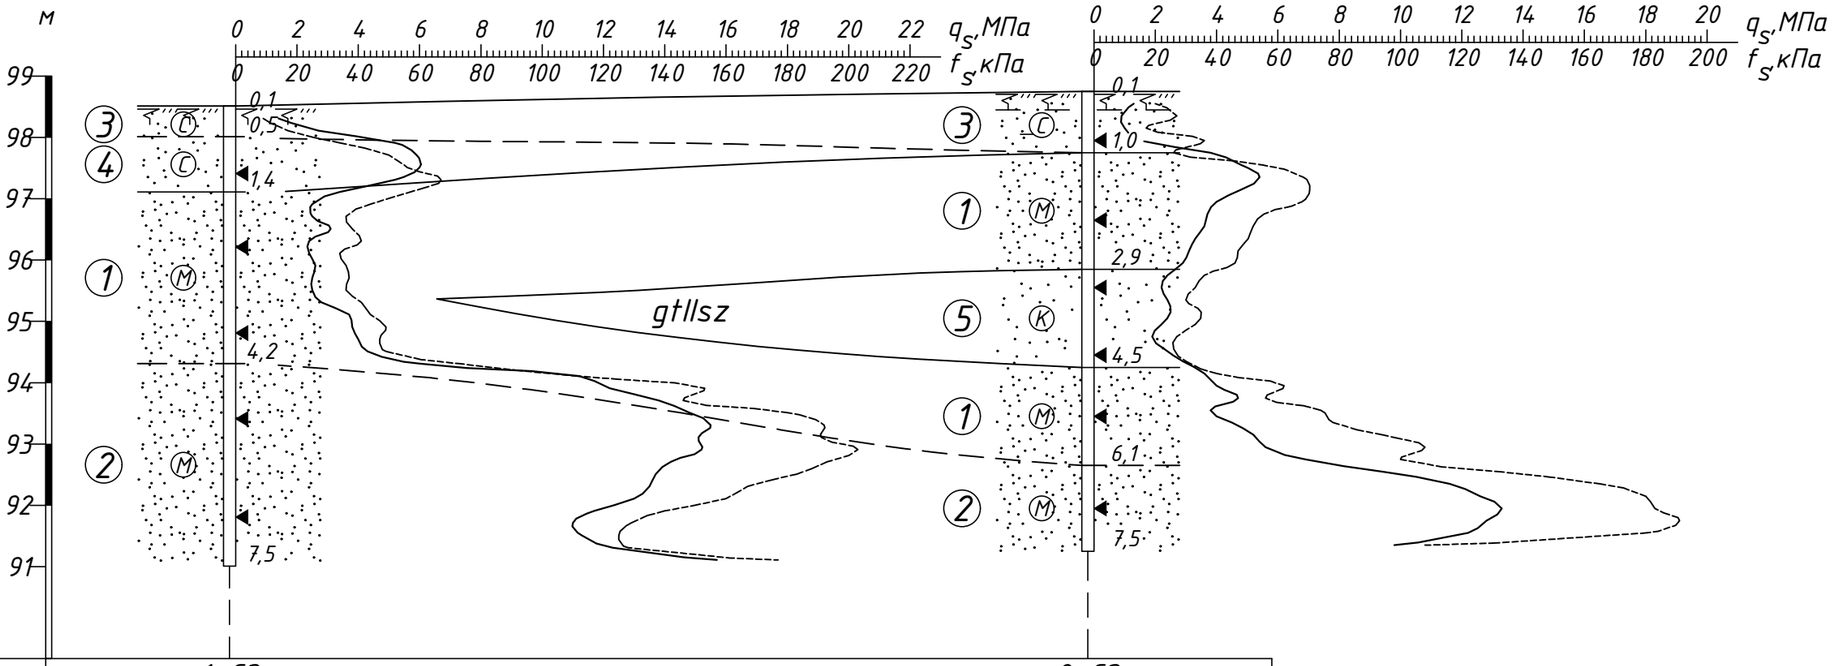


1:100 по горизонтали
1:100 по вертикали

Номер выработки, точки	1, СЗ	2, СЗ
Условная отметка устья, м	98,51	98,75
Расстояние, м	14,0	

① – песок средний средней прочности (γ=16,6кН/м3, Ф=30°, Е=15МПа);
② – песок мелкий прочный (γ=17,9кН/м3, С=3кПа, Ф=35°, Е=33МПа);
③ – песок средний малопрочный (γ=15,6кН/м3);
④ – песок средний средней прочности (γ=17,0кН/м3, Ф=35°, Е=21МПа);
⑤ – песок крупный малопрочный (γ=16,1кН/м3, Ф=32°, Е=15МПа);

Согласовано

Взам. инв. N

Подп. и дата

Инв. N подл.

Изм.	Кол.	Лист	Nдок	Подпись	Дата


...–КЖ

Стадия	Лист	Листов
	1	

Инженерно-геологический разрез

Формат А3

Схема нагрузок на фундаменты на отм 0.000

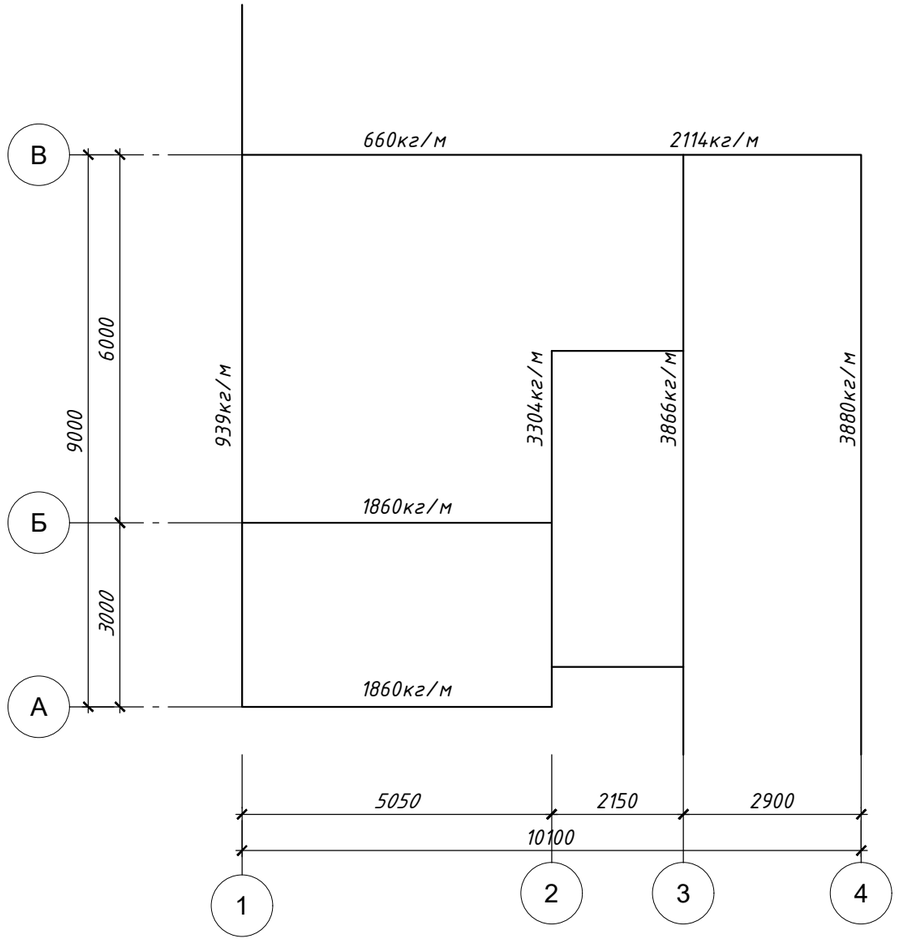

Согласовано

Взам. инв. N

Подп. и дата

Инв. N подл.

Изм.	Кол.	Лист	Nдок	Подпись	Дата


...-КЖ

Стадия	Лист	Листов
	2	


Схема нагрузок на фундаменты на отм 0.000

Формат А3


План ленты фундамента

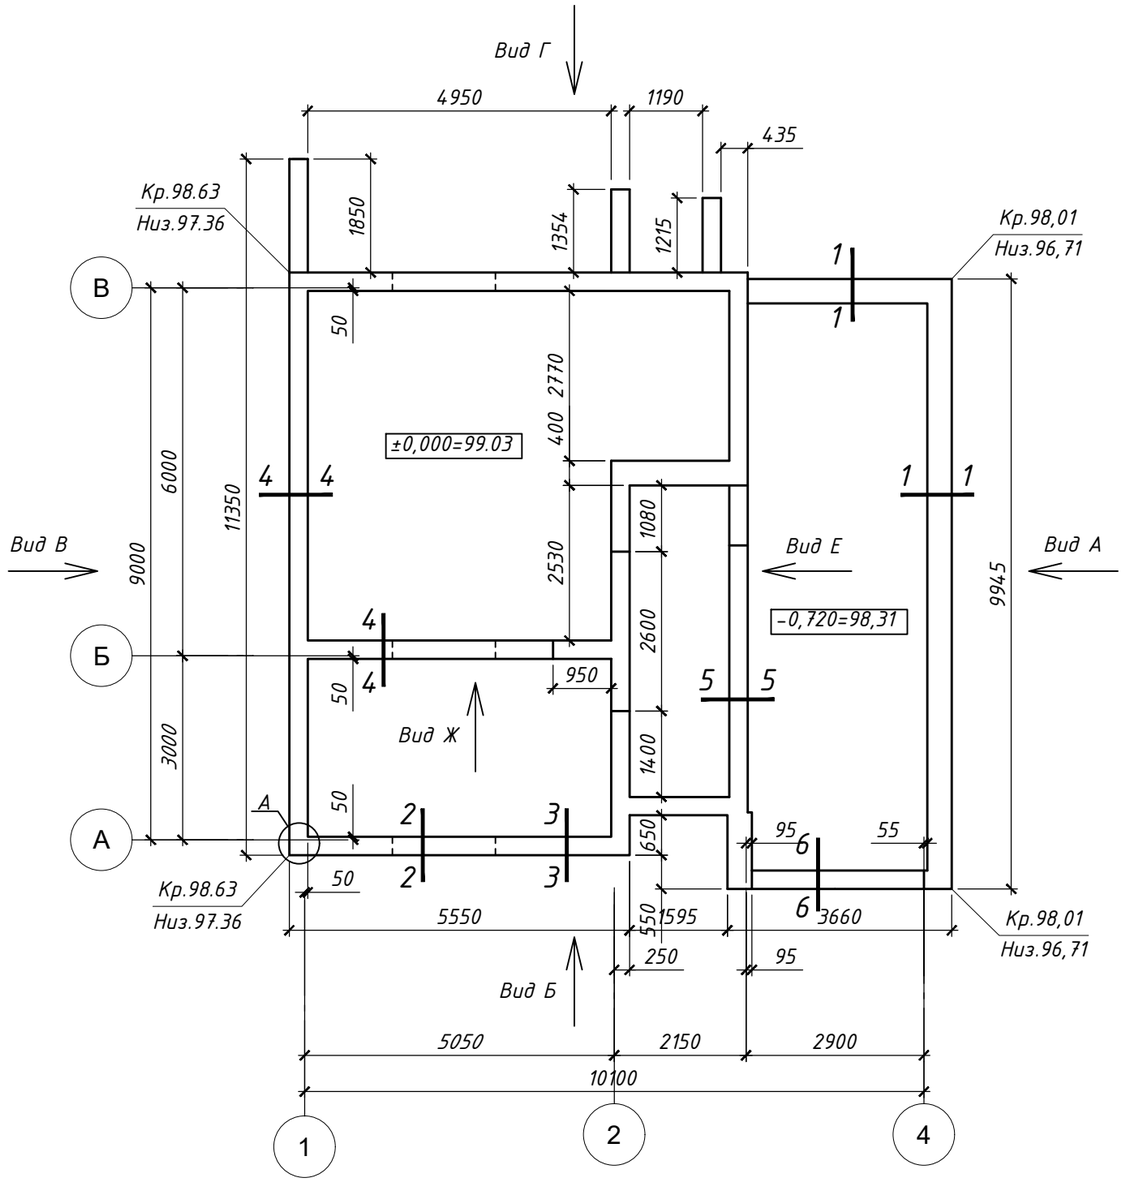


Узел А

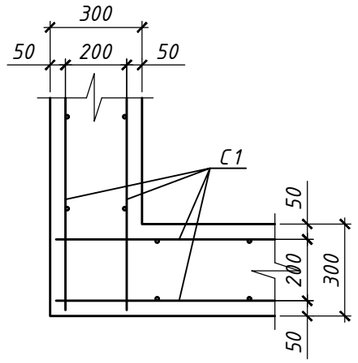


Вид А

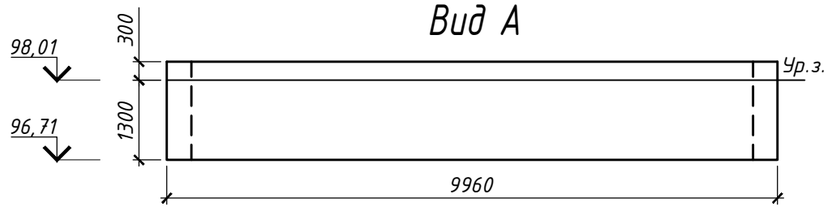


Вид Б

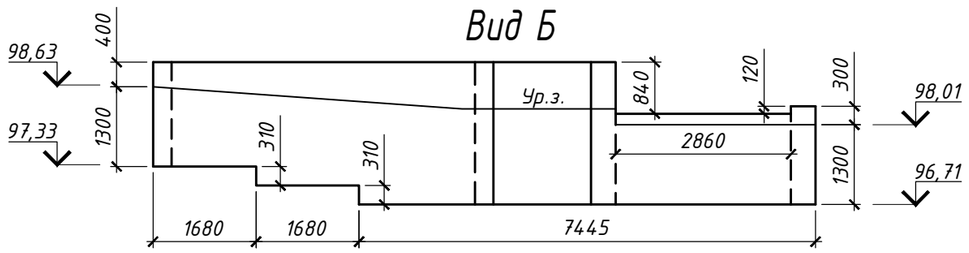

Вид В

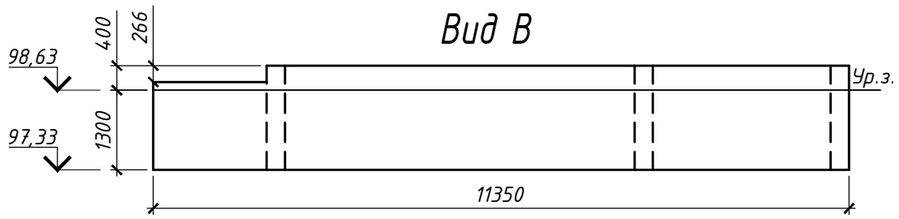

Вид Г

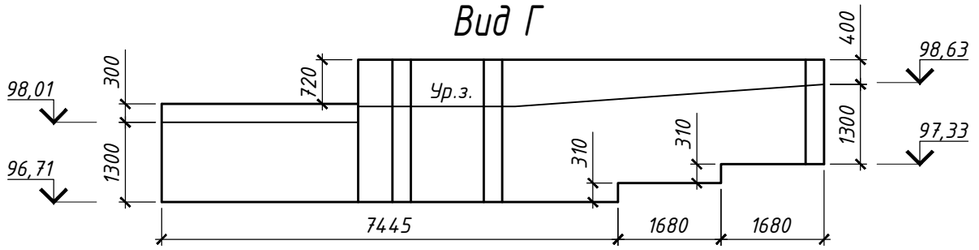

Изм.	Кол.	Лист	Nдок	Подпись	Дата	...-КЖ		
							Стадия	Лист	Листов
								3	
						План ленты фундамента. Вид А, Б, В, Г. Узел А			

Согласовано

Взам. инв. N

Подп. и дата


Инв. N подл.

Формат А3


Вид Е




Вид Ж

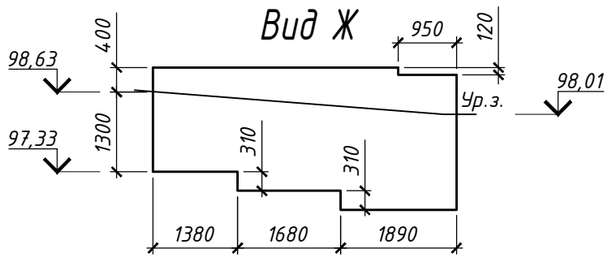


3-3

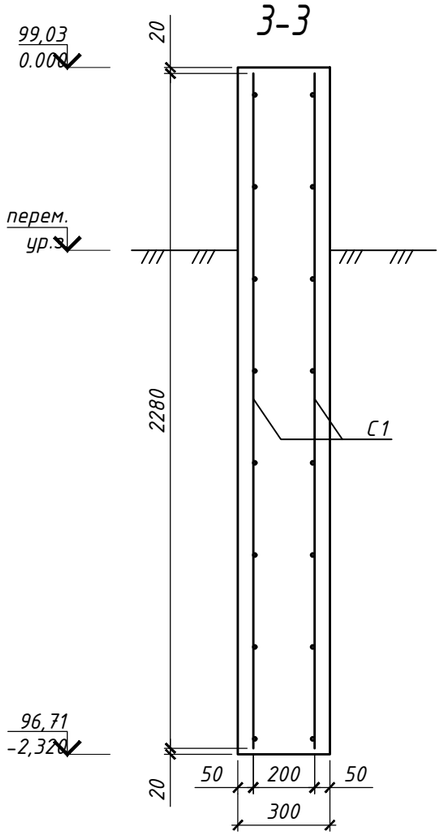


4-4

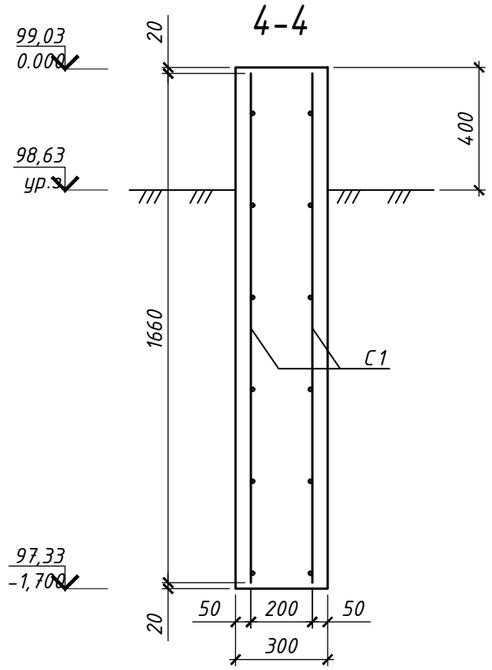

1-1

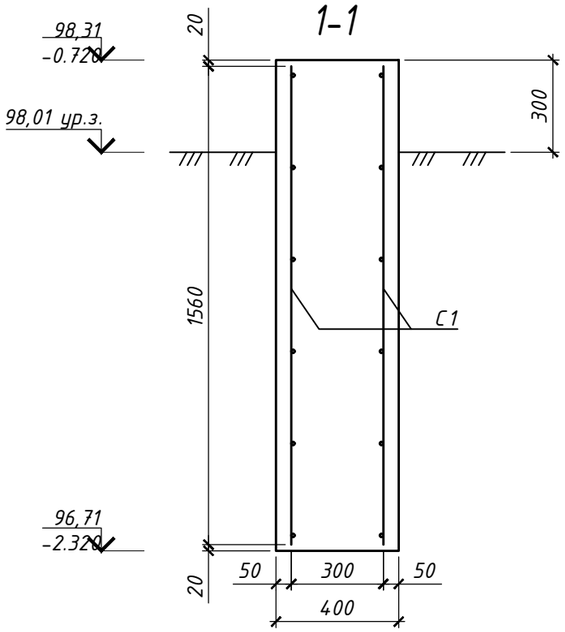

2-2

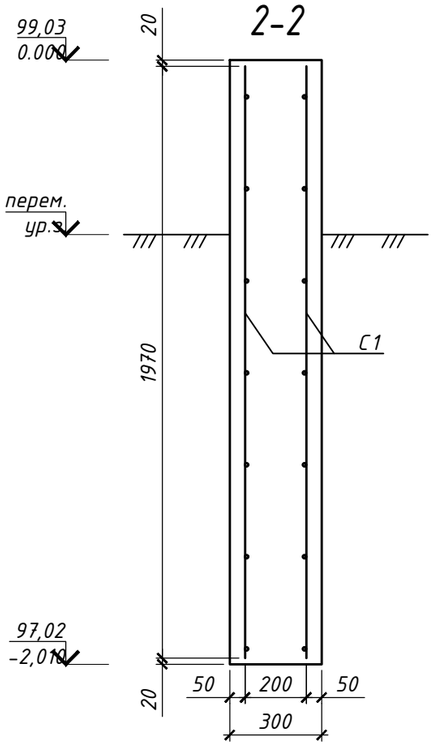

Согласовано

Взам. инв. N

Подп. и дата

Инв. N подл.


Изм.	Кол.	Лист	Nдок	Подпись	Дата


...-КЖ

Стадия	Лист	Листов
	4	

Вид Е, Ж. Сечение 1-1...4-4

Формат А3

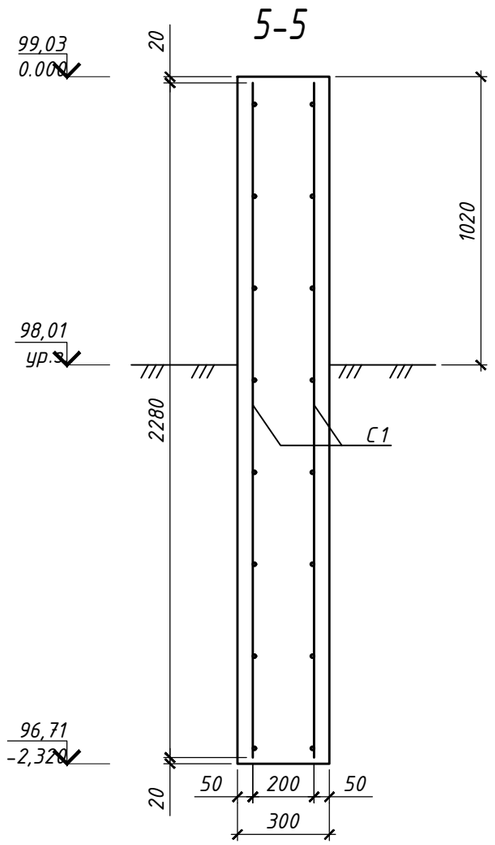

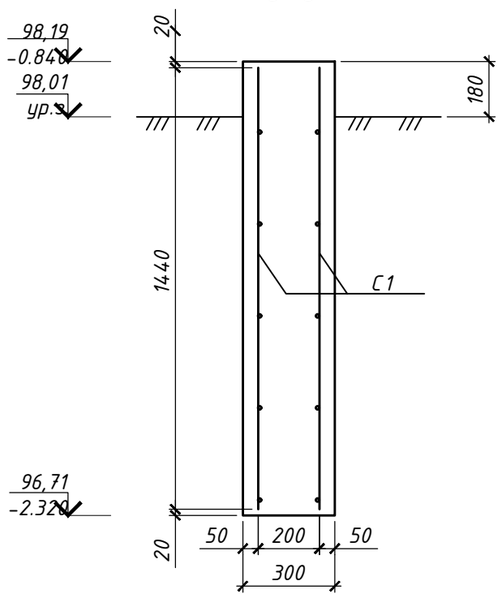

1. За условную отметку 0,000 принят уровень чистого пола первого этажа, что соответствует абсолютной отметке 99,03;

2. Отметка низа фундамента по ИГЭ1 согласно инженерно-геологических изысканий;

3. Обратную засыпку пазух котлована грунтом производить одновременно с двух противоположных сторон стены с перепадом по высоте не более 1м грунтом без строительного мусора и органических примесей слоями толщиной не более 200мм с плотным трамбованием каждого слоя до коэффициента уплотнения не менее 0,95;

4. Монолитные работы вести согласно ТКП 45-5.03-131-2009 "Монолитные бетонные и железобетонные конструкции. Правила возведения.";

5. Позиции армирования смотреть на разрезах фундамента.

Спецификация элементов фундаментов

Поз.	Обозначение	Наименование	Кол.	Масса ед.,кг.	Примеч.
С1		Сетка 4С $\frac{6S500-200}{6S500-200}$ 260м2		568,2	
		Материалы			
		Бетон С16/20 F100	40,2		$м^3$

Примечание:

1. Соединять арматуру сваркой не производить, соединения арматуры между собой производить при помощи вязальной проволоки;

2. Бетонную смесь укладывать в опалубку горизонтальными слоями без технологических разрывов;

3. Бетонная смесь, потерявшая к моменту укладки заданную удобоукладываемость, подаче в бетонируемую конструкцию не подлежит. Восстанавливать удобоукладываемость бетонной смеси добавлением воды на месте укладки запрещается.

4. Следующий слой бетонной смеси необходимо укладывать до начала схватывания бетона в предыдущем уложенном слое. Если, перерыв в бетонировании превысил время начала схватывания бетона в уложенном слое, необходимо устроить рабочий шов.

5. Открытые поверхности свежеуложенного бетона после окончания бетонирования предохранить от испарения воды.

6. Свежеуложенный бетон защитить от попадания атмосферных осадков. Защита открытых поверхностей бетона должна быть обеспечена в течение срока, обеспечивающего приобретение бетоном прочности не менее 70% (при температуре +20С - 7 суток).

Согласовано

Взам. инв. N


Подп. и дата


Инв. N подл.


Изм.	Кол.	Лист	Nдок	Подпись	Дата	...-КЖ		
							Стадия	Лист	Листов
								5	
						Сечение 5-5, 6-6			

Формат А3

Схема расположения несущих элементов под устройства веранды

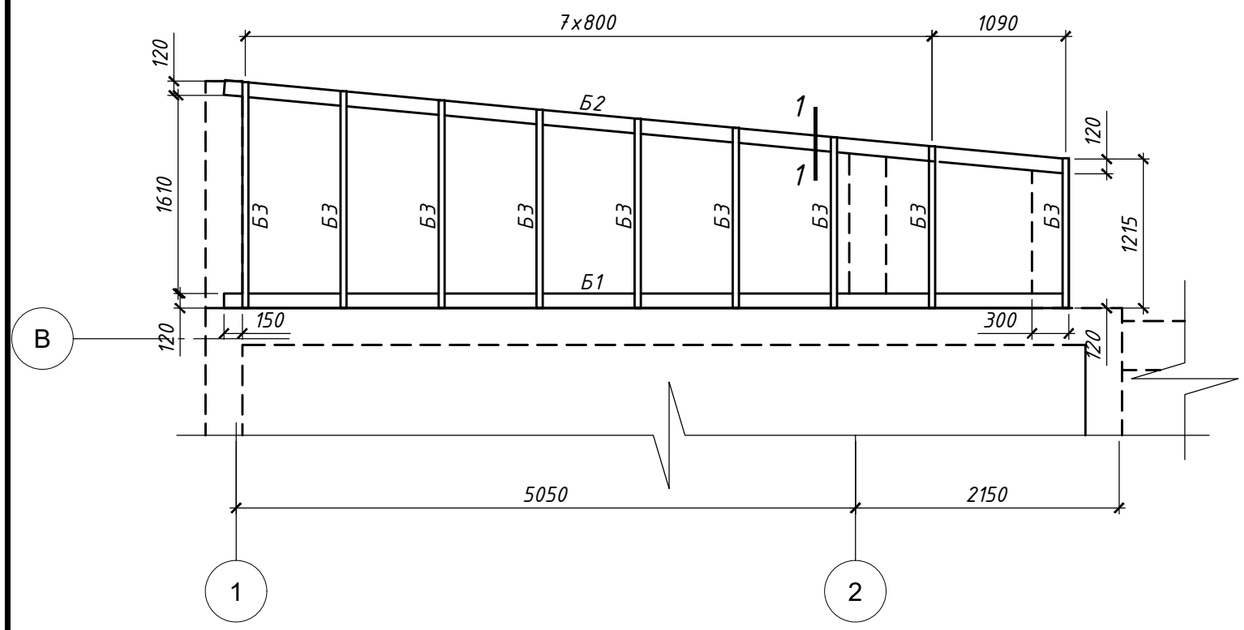

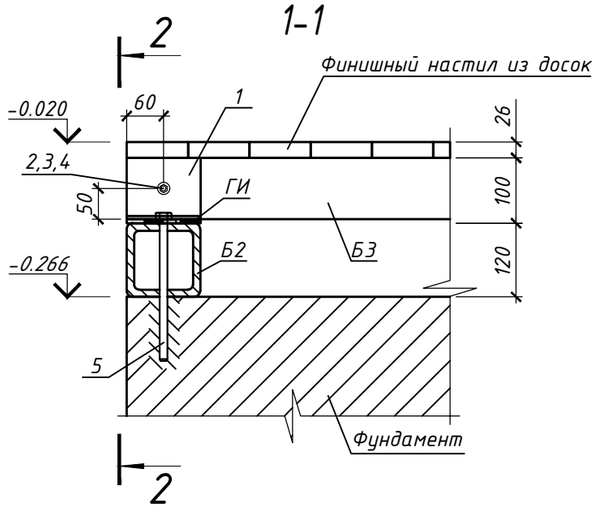

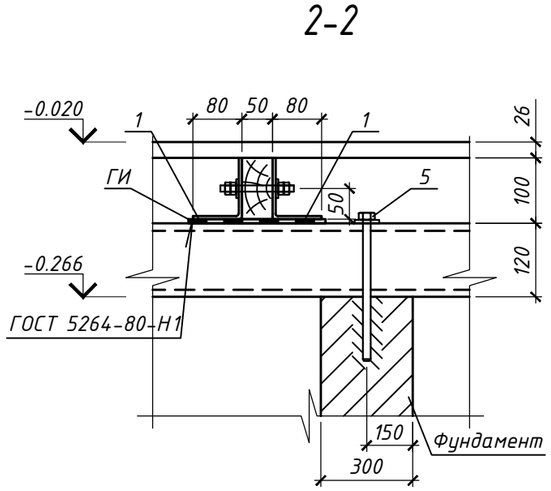

Спецификация элементов

Поз.	Обозначение	Наименование	Кол.	Масса ед.,кг.	Примеч.
Б1		□120х6 ГОСТ 30245-2003 / С245 ГОСТ 27772-88* L=6890	1	148,8	
Б2		□120х6 ГОСТ 30245-2003 / С245 ГОСТ 27772-88* L=6910	1	148,4	
Б3	СТБ 1713-2007	Прогон 100(h)х50 Lобщ=13900			0.07м3
1	...-КЖи.Д1	Деталь Д1	18	0,85	
2	СТБ 1704-2006	Ф8 S240 L=100	9	0,04	
3	ГОСТ 5915-70	Гайка М8	18		
4	ГОСТ 11371-68*	Шайба М8	18		
5		Распорный анкер 10х180	6		
	Заглушка	Лист 6х120х120 ГОСТ19903-74* / С235 ГОСТ 27772-88	4	0,68	

1.Финишный настил выполнять по схеме неразрезной двухпролётной балки.

2.Деревянные элементы обработать огнебиозащитным составом ОК-ГФМ плотностью раствора 1150кг/м^3 (средний расход 0,28кг/м^2) для получения II группы огнезащитной эффективности по ГОСТ 30219-95. Проведение работ с применением огнезащитных составов является лицензируемым видом деятельности. Металлические элементы окрасить двумя слоями эмали ПФ-115 ГОСТ 6465-76 по слою грунтовки ГФ-021 ГОСТ 25129-82

3.Для изготовления несущих конструкций из дерева применять пиломатериалы II сорта из хвойных пород по СТБ 1713-2007 (в части размеров) влажностью не более 20%.

4.Деревянные элементы и изделия построечного изготовления должны отвечать требованиям СТБ 1713-2007 в части предельных отклонений размеров, влажности и допускаемых пороков древесины.

5.На период производства работ деревянные конструкции следует оберегать от увлажнения и замачивания.

6. В местах соприкасания деревянных элементов с металлическими изделиями поверхность элементов перед монтажом покрыть эмалью ПФ-115, нанесенной в 2 слоя, после подсушки указанный участок обернуть 1 слоем материала Г-СТ-БП-ПП/ПП-3.5 СТБ 1107-98 (площадь 0,5м^2).

7. Все замкнутые профили должны быть герметизированы путем соединения элементов в замкнутое сечение и заварки прорезей сплошными швами, предотвращающими попадание влаги внутрь этих элементов.

Изм.	Кол.	Лист	Nдок	Подпись	Дата	...-КЖ		
							Стадия	Лист 6 / Листов
						Схема расположения несущих элементов под устройства веранды		


Согласовано

Взам. инв. N


Подп. и дата

Инв. N подл.

Формат А3

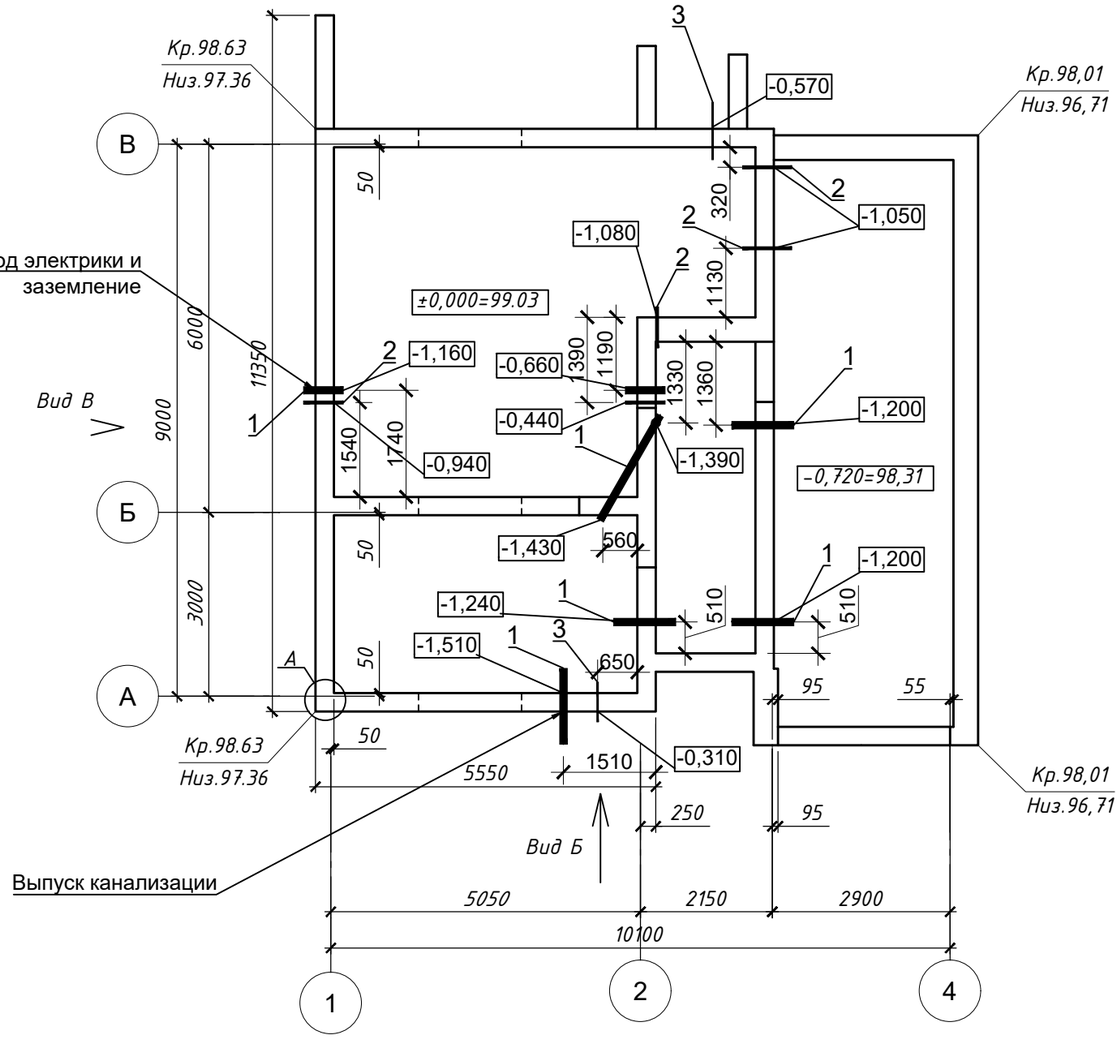

Узел устройства поливочного крана

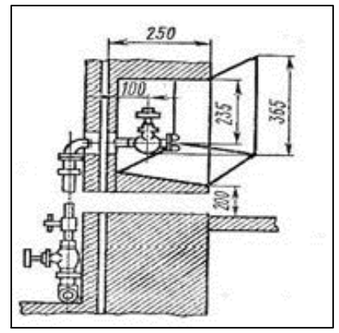

1. гильза под трубу Ø 110мм
2. гильза под трубу Ø 50мм
3. гильза под трубу Ø 25мм (поливочный кран)

Изм.	Кол.	Лист	Nдок	Подпись	Дата	...-КЖ		
							Стадия	Лист	Листов
								7	
						План закладки гильз для коммуникаций			


Согласовано


Взам. инв. N

Подп. и дата

Инв. N подл.

Формат А3

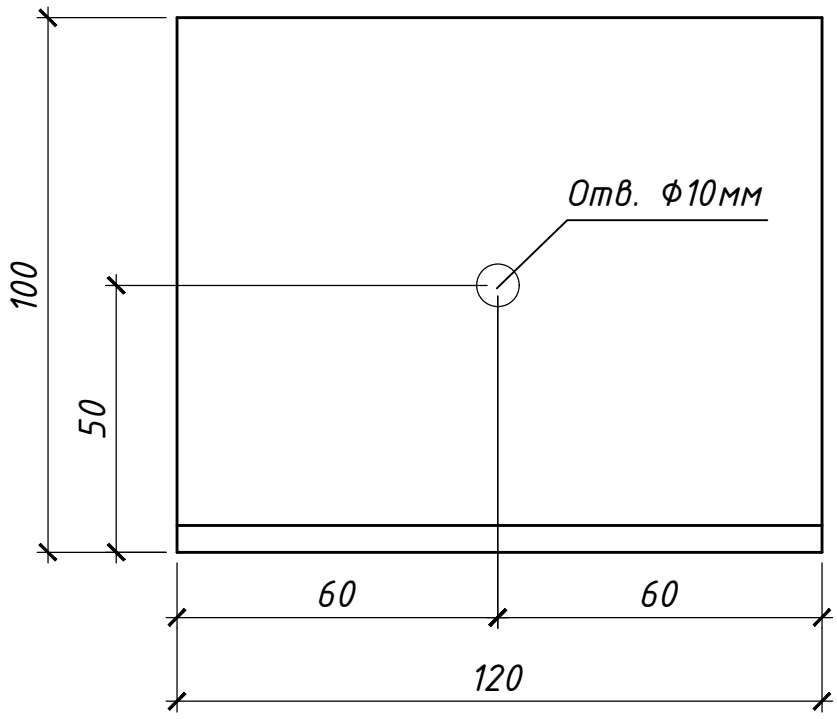

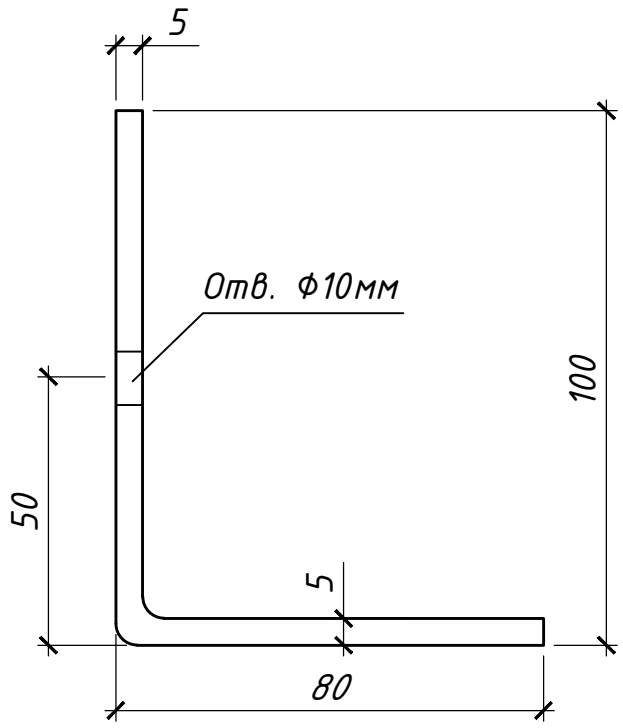

Марка изделия	Поз. дет.	Наименование	Кол.	Масса 1 дет., кг	Масса изделия, кг
Д1	1	Лист $\frac{\text{Лист } 5x120x180}{\text{С245 ГОСТ 27772-88*}}$	1	0.85	0.85

1. Стальные элементы окрасить эмалью ПФ-115 ГОСТ 6465-76 в два слоя по грунтовке ГФ-021 ГОСТ 25129-82 общей толщиной 80 мкм.

Взам. инв. N

Подпись и дата

Инд. N подл.

Изм.	Кол.	Лист	Nдок.	Подпись	Дата

...-КЖи.Д1

Деталь Д1

Стадия	Масса	Масштаб
С	см. спец.	

Лист	Листов

Формат А4