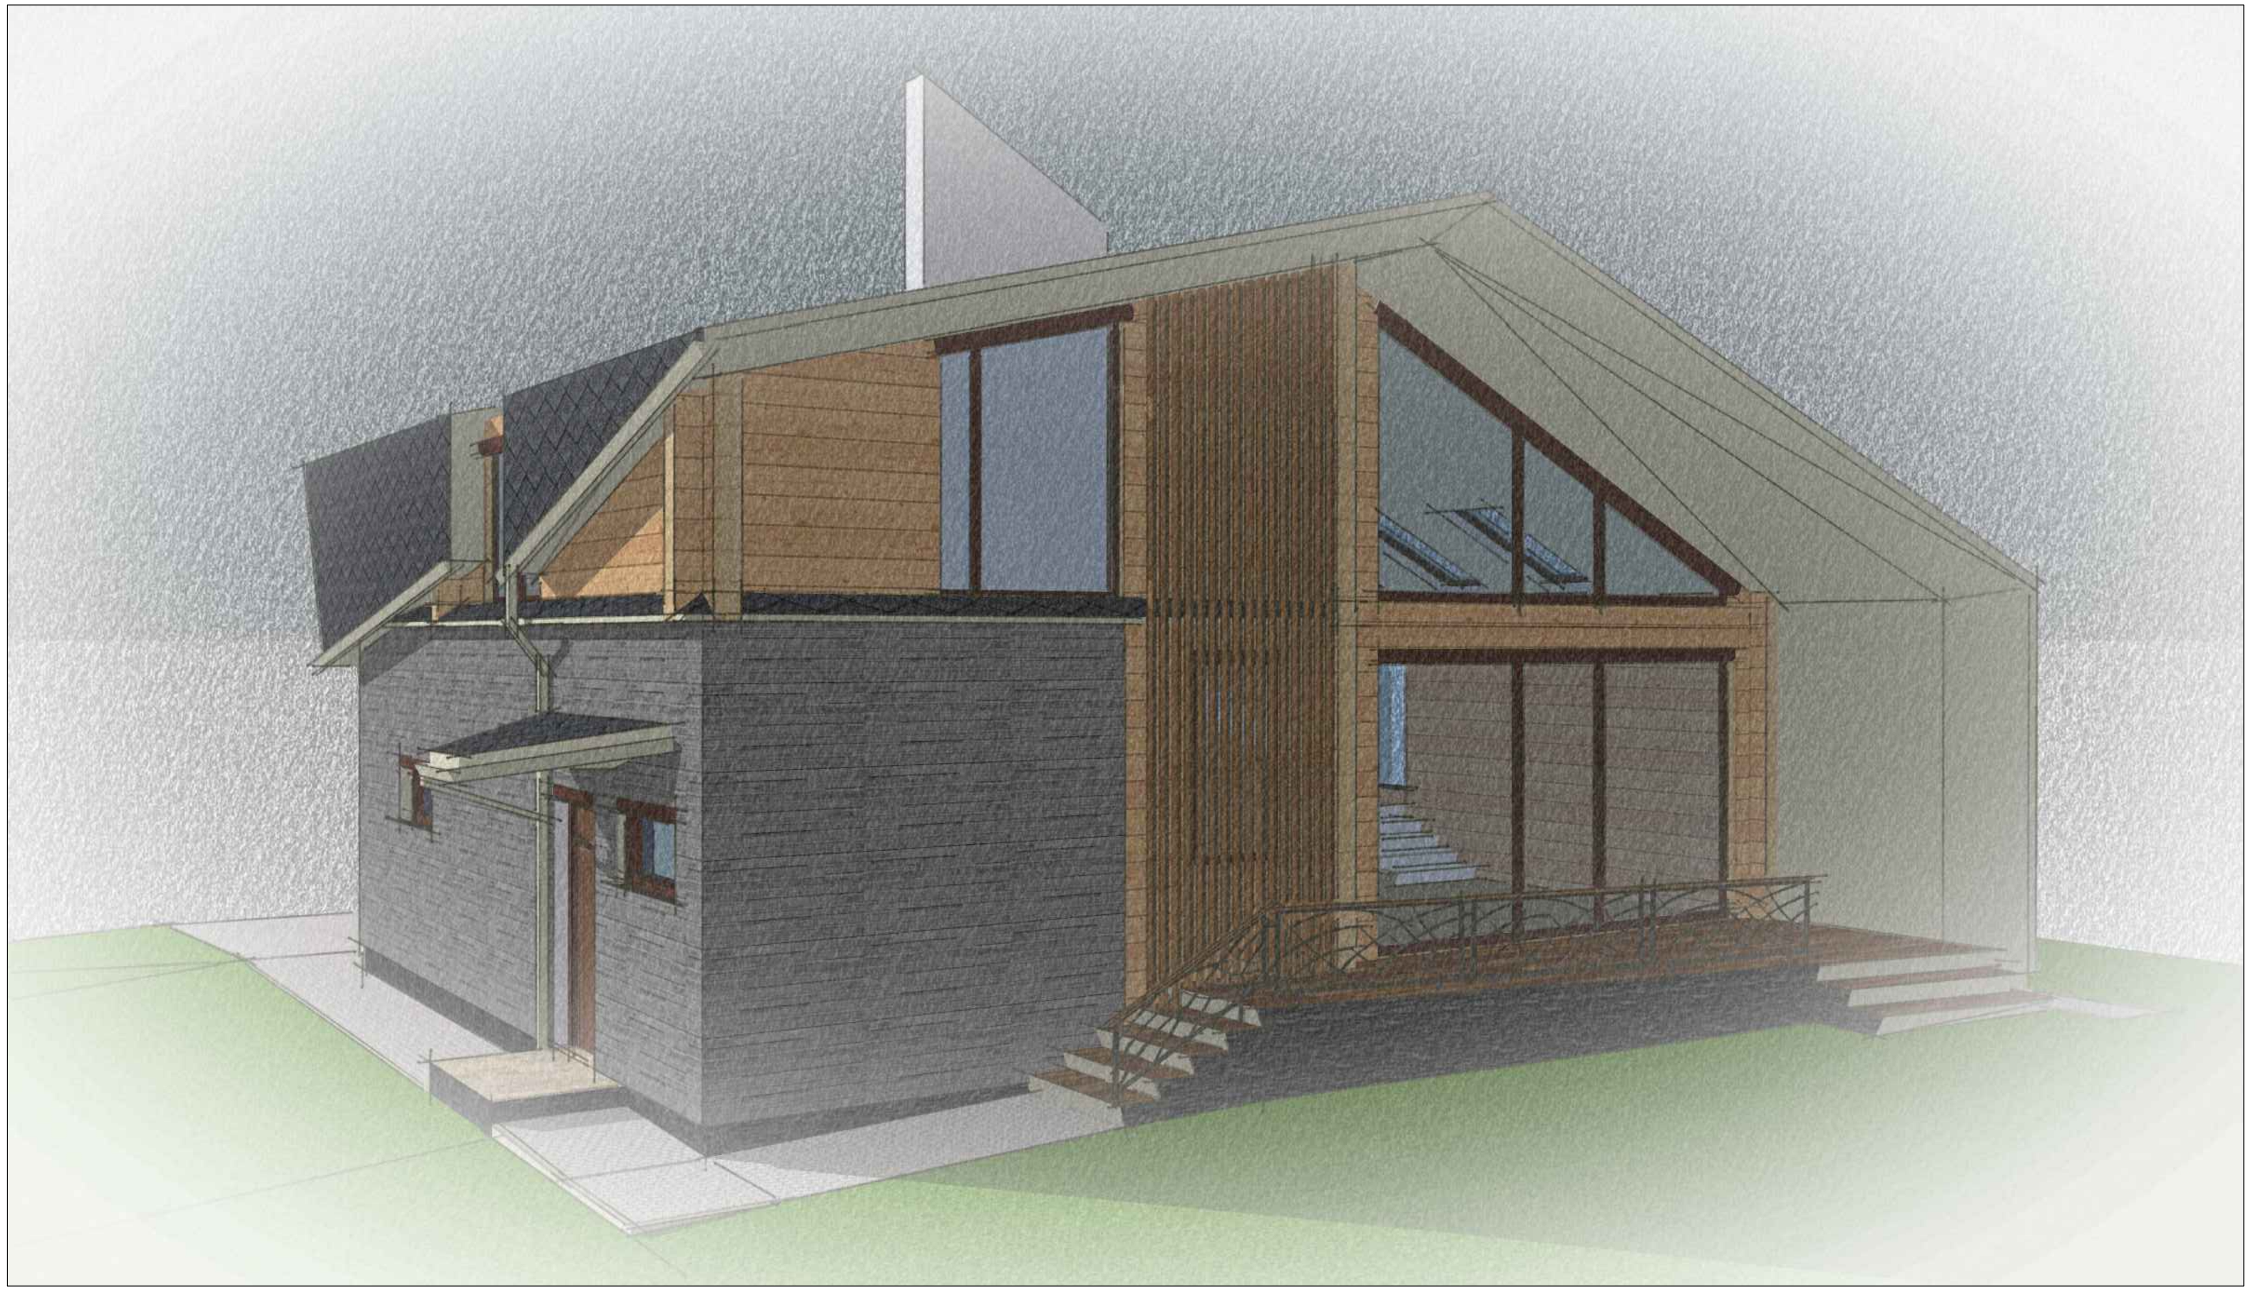

Строительство жилого дома, расположенного по адресу: Минская область, Смолевичский район

Взам. инв. №

Подп. и дата

Инв. № подл.

Ведомость рабочих чертежей основного комплекта

Лист	Наименование	Примечание
1	Общие данные	
2	Генеральный план участка	
3	Архитектурная визуализация здания	
4	План 1-го этажа; План мансардного этажа.	
5	План кровли; Разрез 1-1.	
6	Фасады здания	
7	План размещения мебели 1-го и мансардного этажа.	

ОБЩИЕ УКАЗАНИЯ

1. Строительный проект разработан в соответствии с техническим регламентом «Здания и сооружения, строительные материалы и изделия. Безопасность», актами законодательства Республики Беларусь, межгосударственными и национальными ТНПА, с соблюдением технических условий.

2. Производство работ вести согласно требованиям СНиП 3.04.01-87 "Изоляционные и отделочные работы", СНиП 3.03.01-87 "Несущие и ограждающие конструкции", ТКП 45-5.09-33-2006 (02250) "Антикоррозионные покрытия строительных конструкций зданий и сооружений. Правила устройства", ТКП 45-1.03-40-2006 (02250) "Безопасность труда в строительстве. Общие требования".

3. Все материалы, изделия, конструкции и оборудование, применяемые в строительстве по чертежам данного комплекта должны иметь свидетельства о проведении обязательной сертификации на соответствие требованиям пожарной безопасности.

4. Проектом предусматривается строительство жилого дома, расположенного по адресу: Минская область, Смолевичский район,

В конструктивном отношении здание с несущими наружными и внутренними продольными стенами и деревянными перекрытиями.

- Степень огнестойкости здания - не ниже VII по ТКП 45-2.02-142-2011.
- Класс по функциональной пожарной опасности Ф1.4. (по ТКП 45-2.02-142-2011)
- Класс сложности здания - К5 по СТБ2331-2014

5. За отметку +0,000 принят уровень проектируемого чистого пола 1-го этажа в пом."2" .

6. При пересечении стен и перегородок инженерными коммуникациями зазоры между коммуникациями и преградами тщательно зачеканить цементно-песчаным раствором М75 на всю толщину стены.

7. Устройство полов выполнять после монтажа инженерных и технологических коммуникаций.

8. Перед выполнением монтажа оборудования необходимо закончить все строительные работы. Помещения должны быть убраны и свободны от посторонних предметов. После установки оборудования не рекомендуется проводить покрасочные и прочие отделочные работы, ремонт полов, устройство перегородок и т.п. Все стальные элементы (кроме оцинкованных) окрасить двумя слоями эмали ПФ-115 ГОСТ 6465-76 по слою грунта ГФ-021 ГОСТ 25129-82. Минимальная толщина покрытия 55мкм.

9. Технико-экономические показатели:

9.1 Общая площадь - 155,0$м^2$

9.2 Строительный объем - 465,0 $м^3$

Взам. инв. №

Подп. и дата

Инв. № подл

-АР

	1	7

Общие данные

Копировал

А3

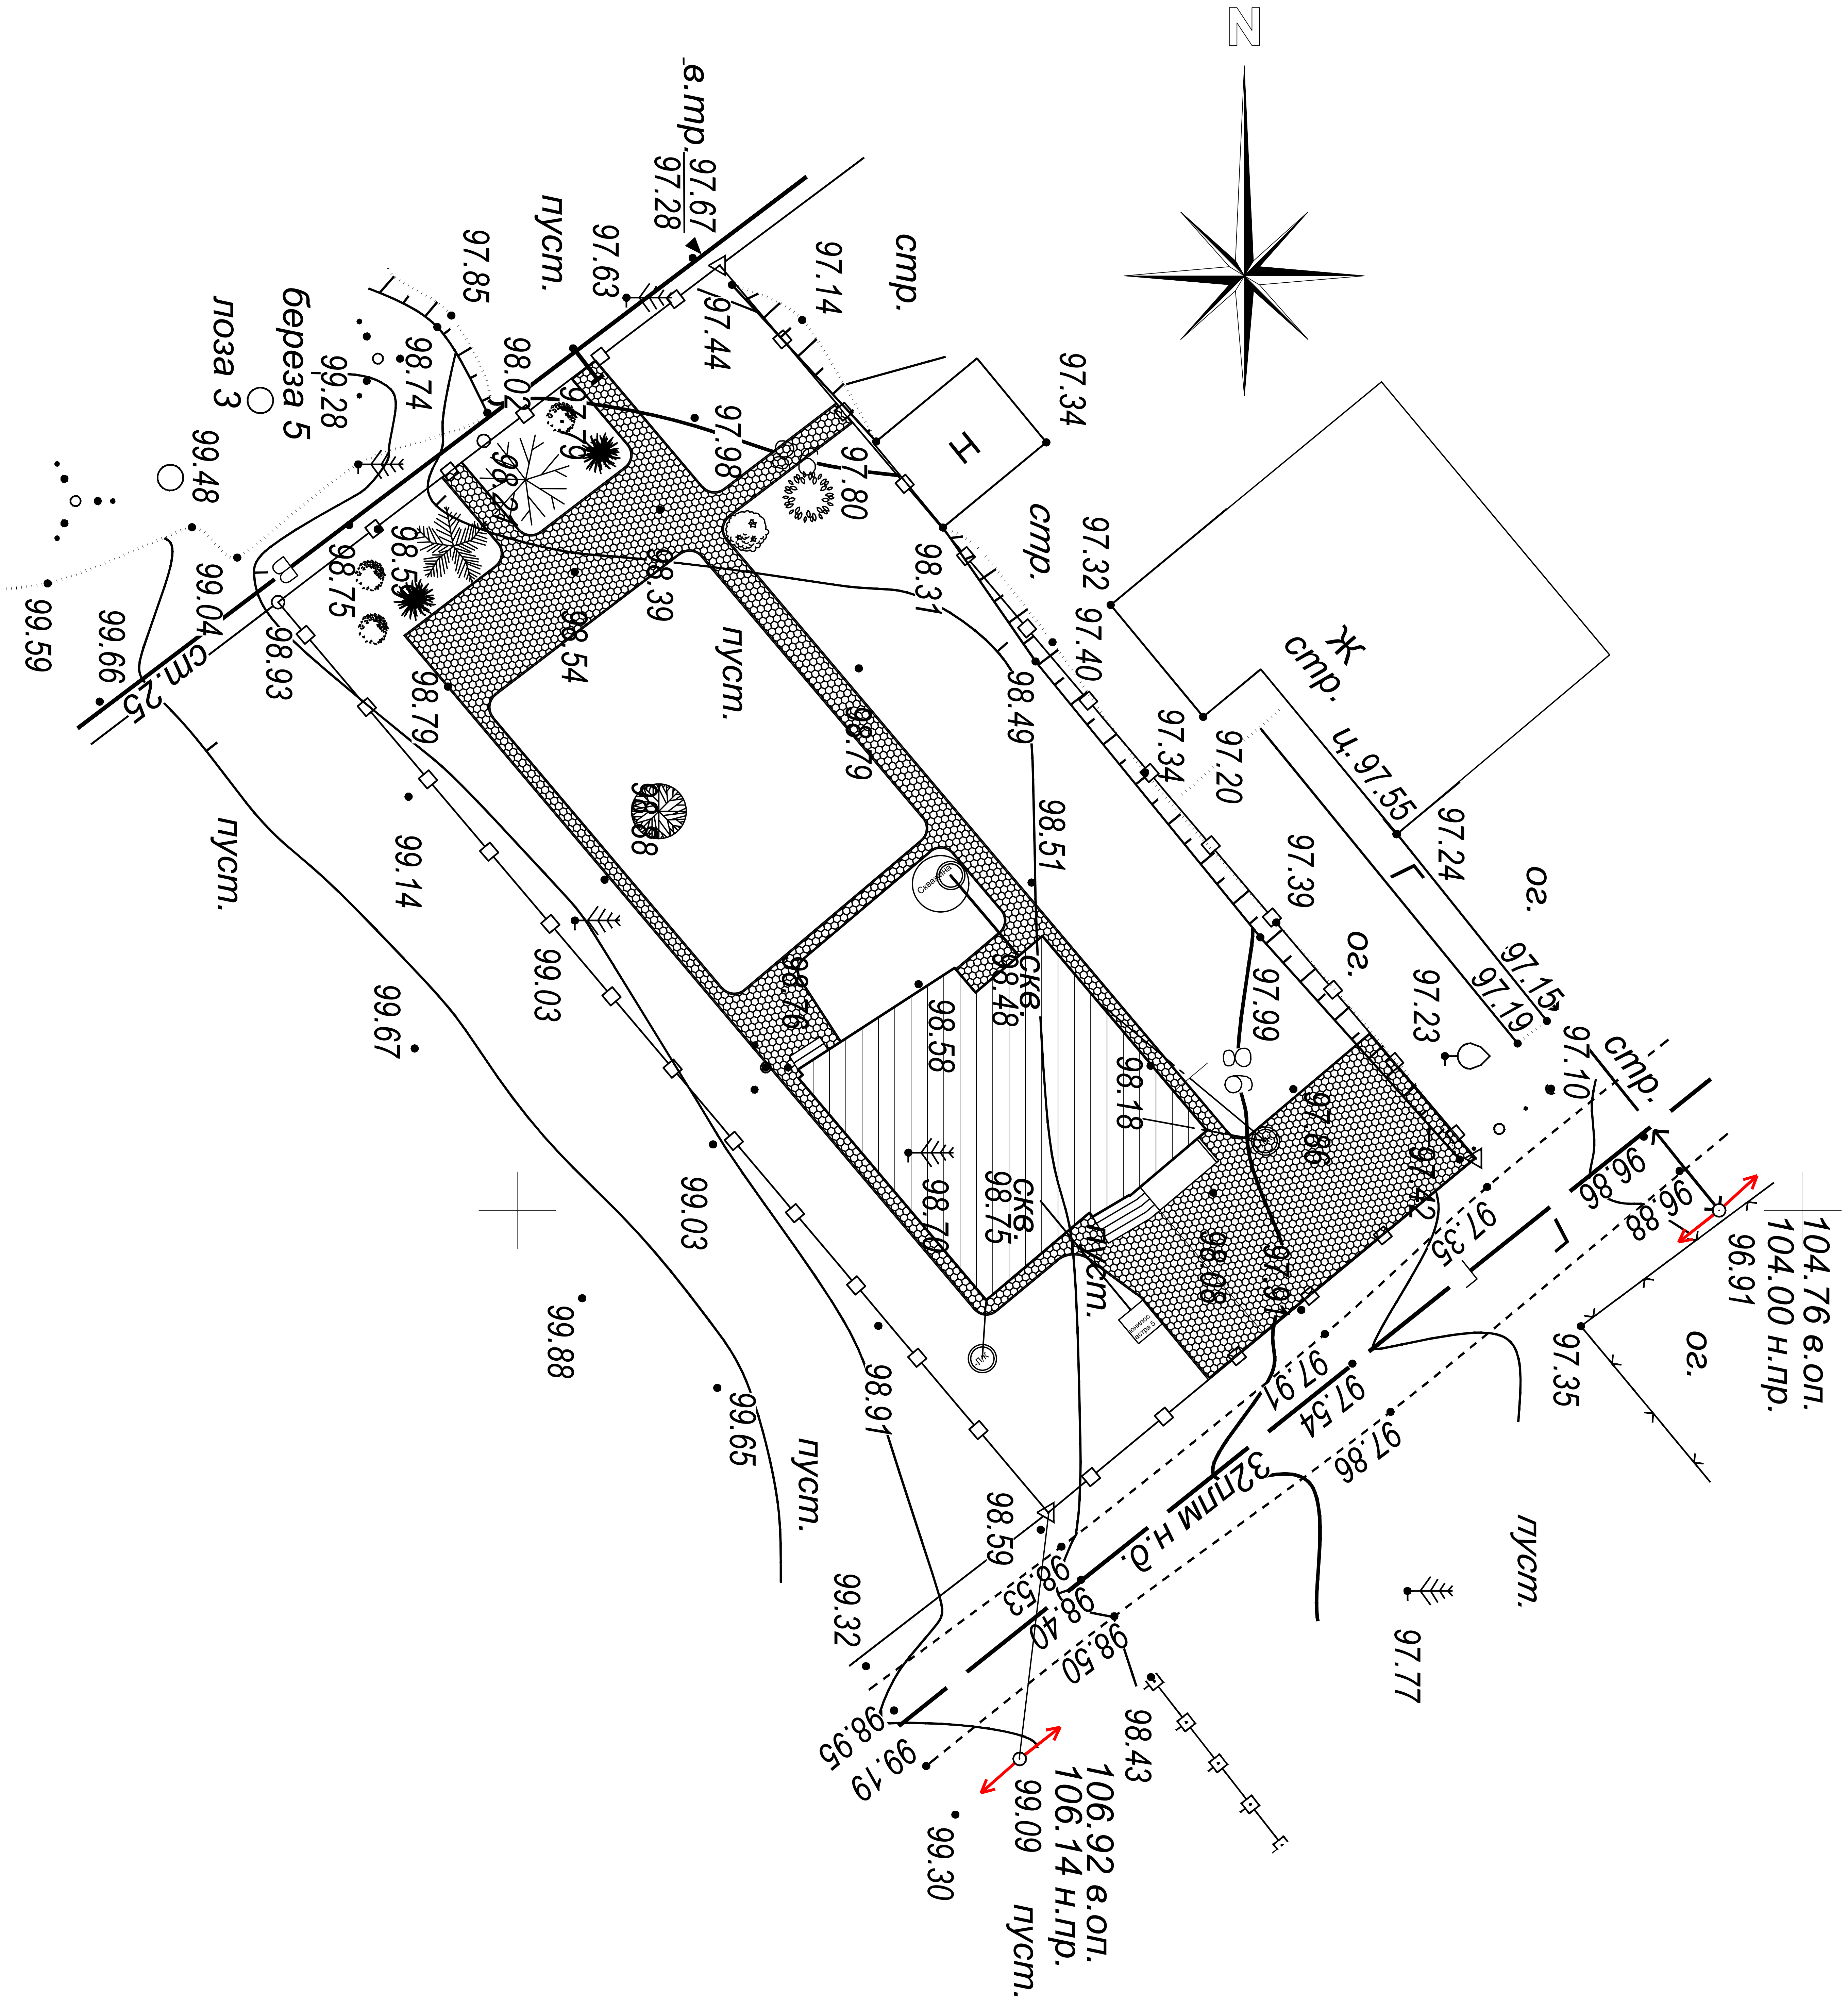

Взам. инв. №

Подп. и дата

Инв. № подл

-АР

2

Генеральный план участка
М 1:500

Копировал

А3

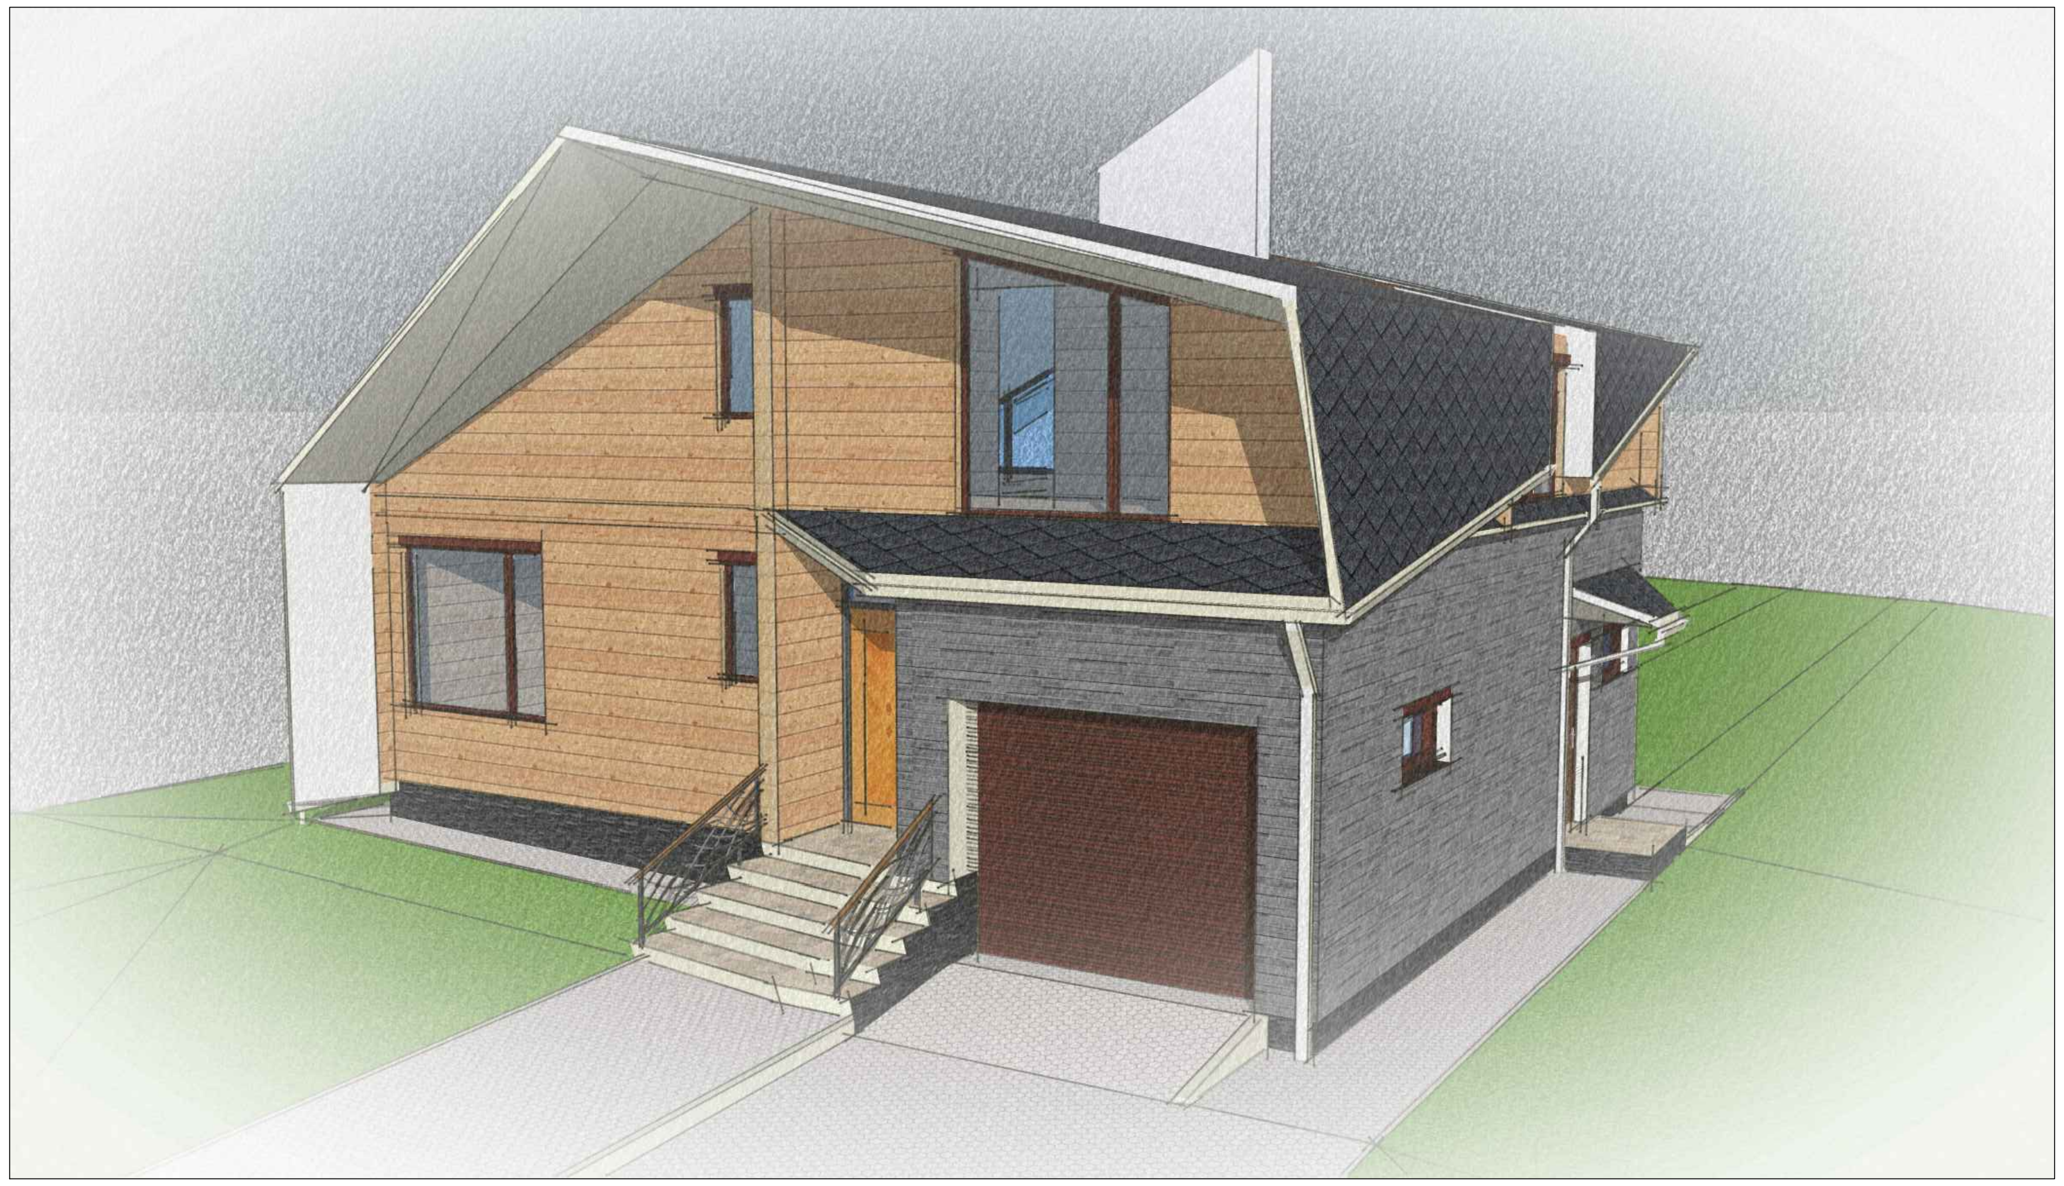

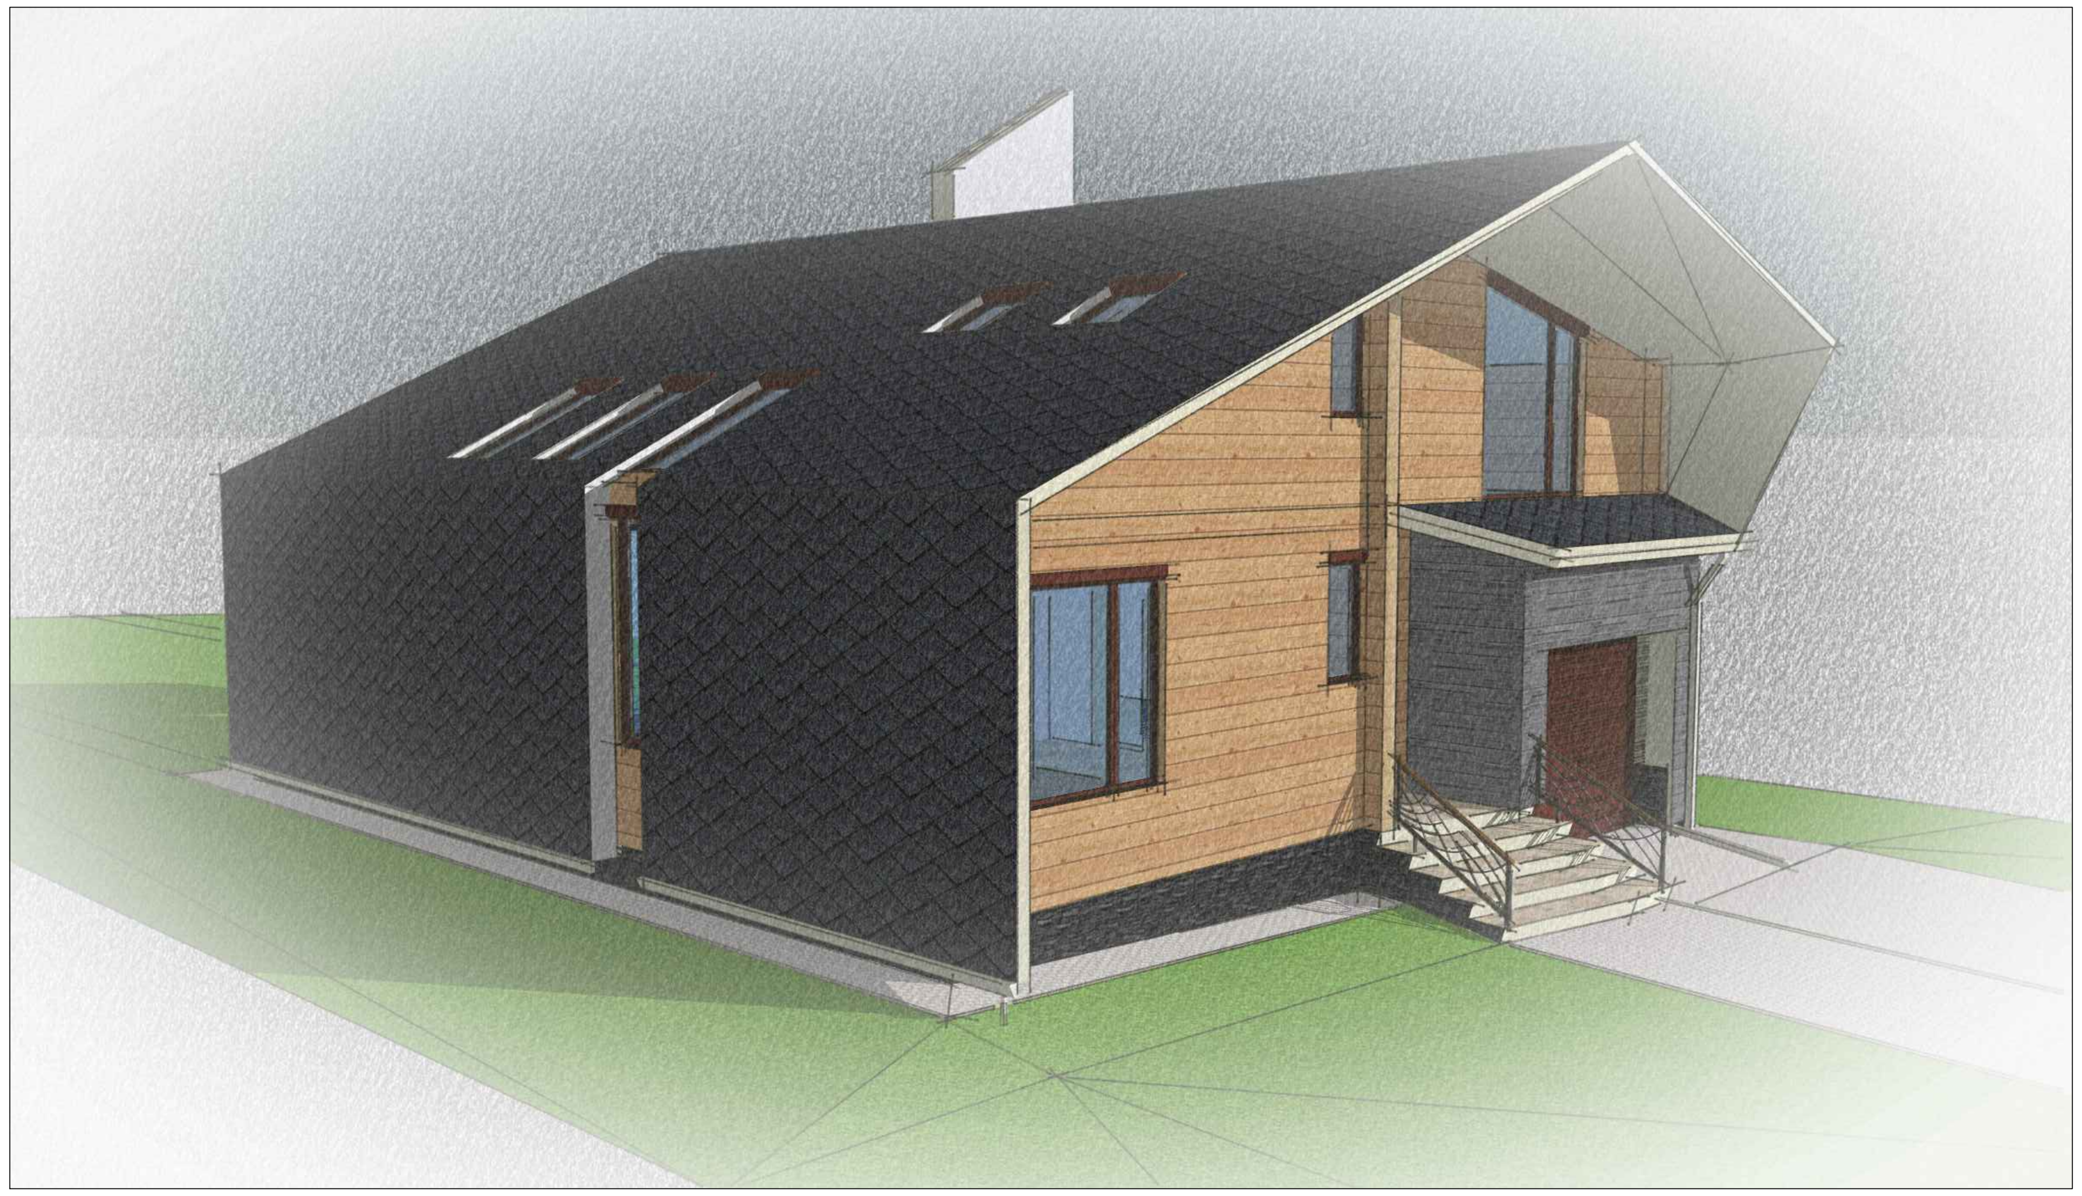

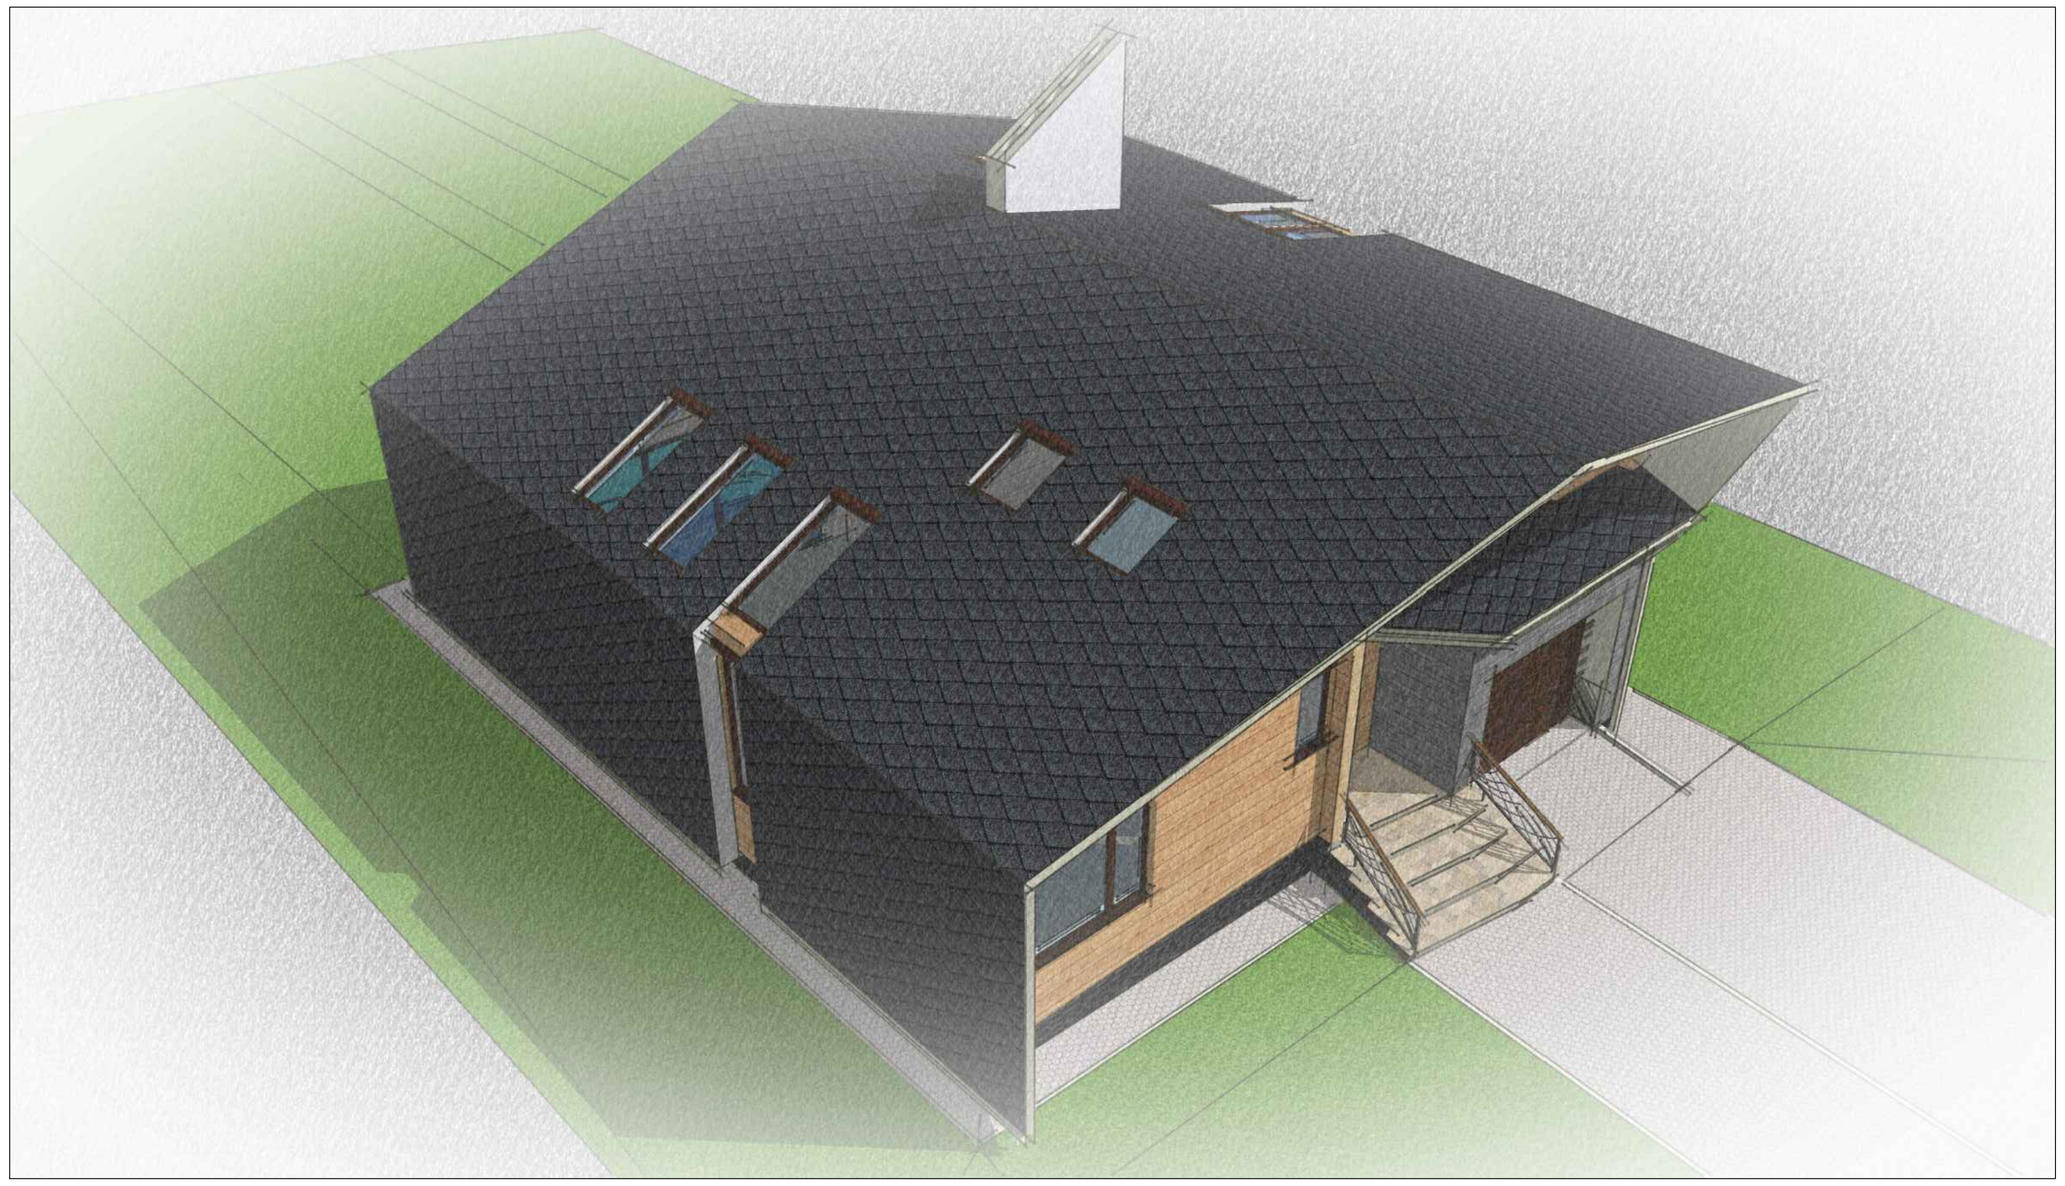

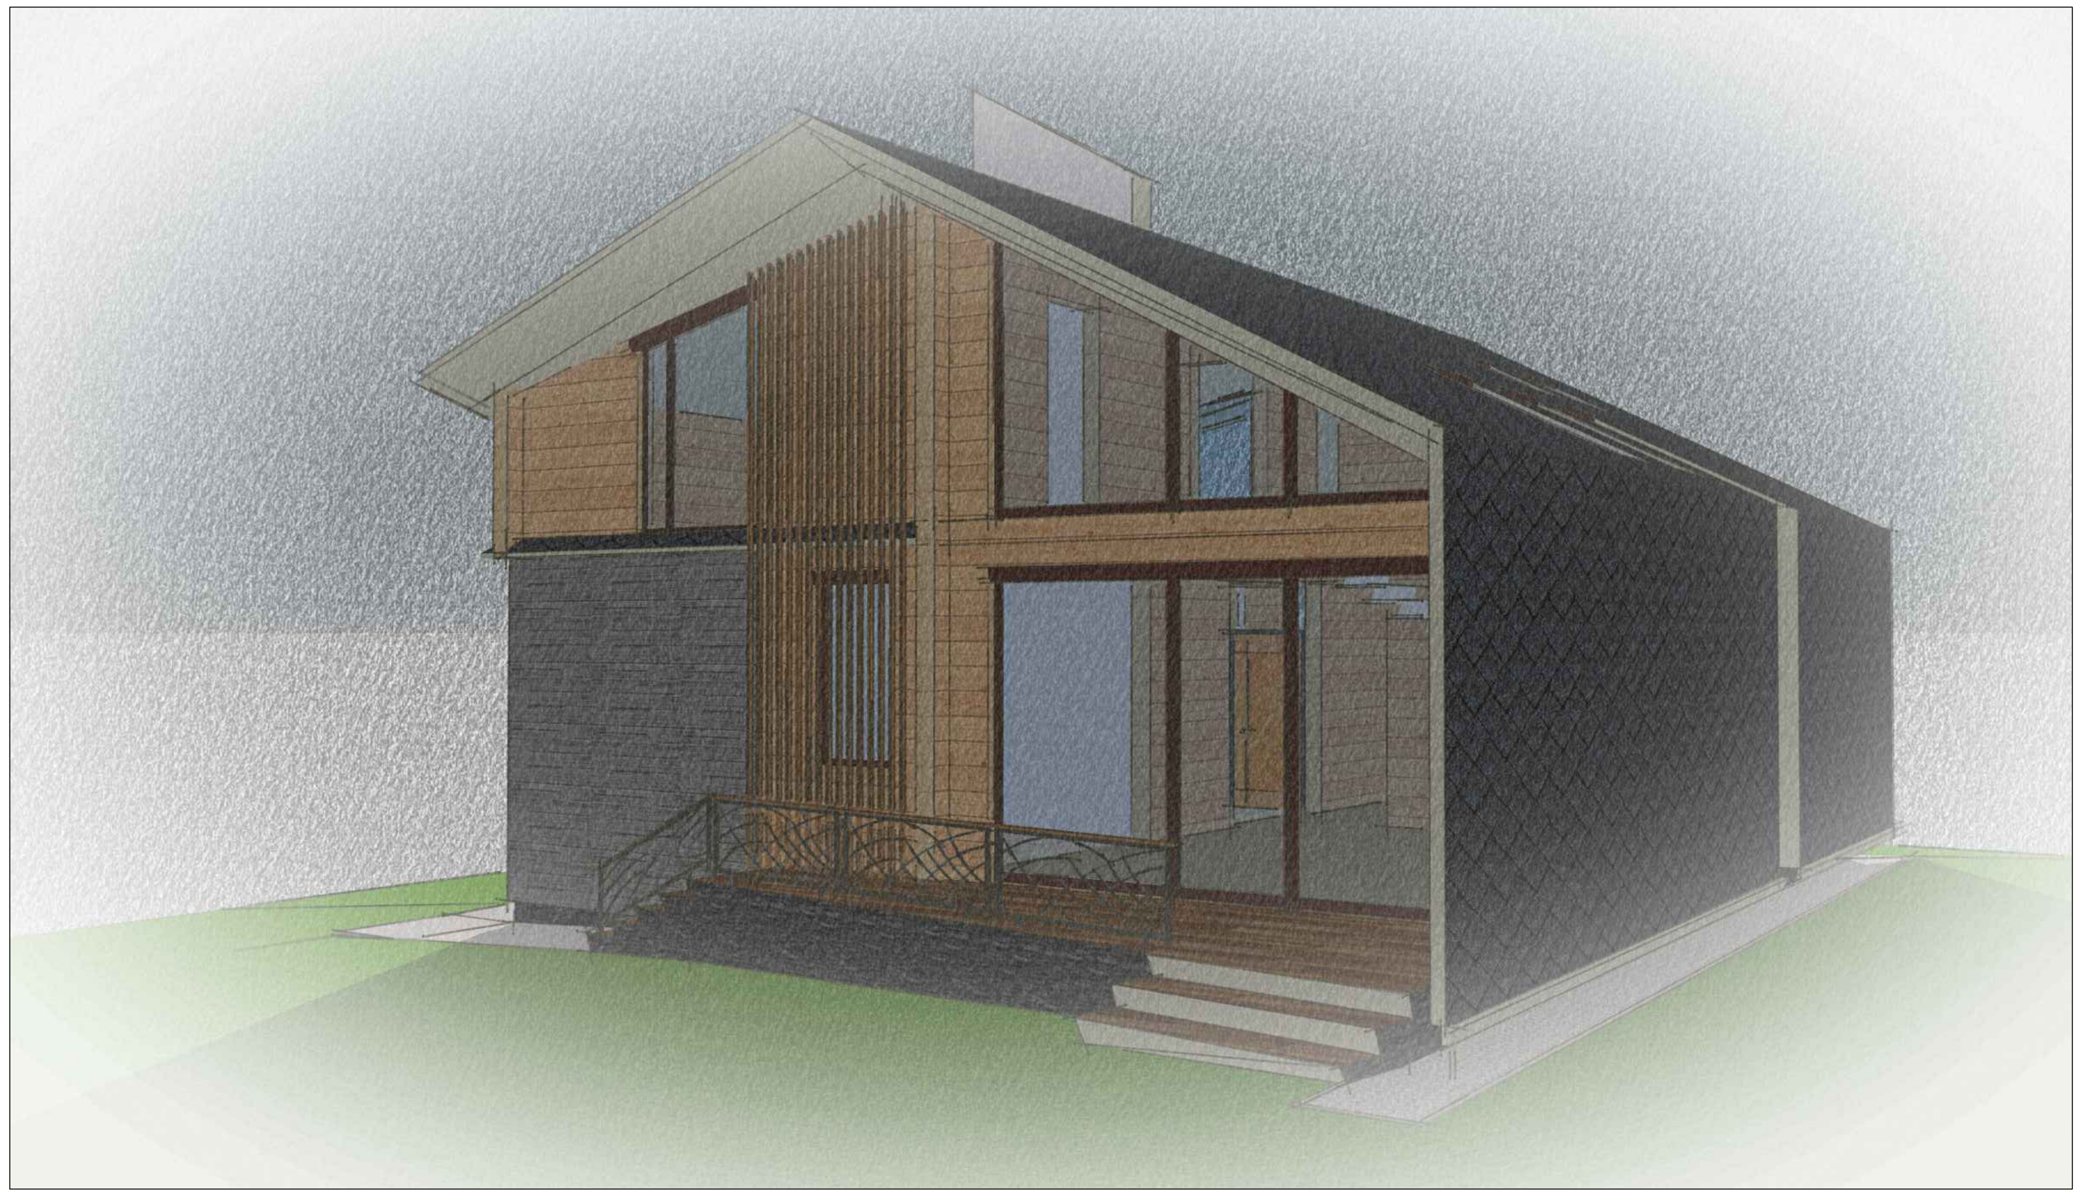

Взам. инв. №

Подп. и дата

Инв. № подл.

-АР

3

Архитектурная визуализация здания

План 1-го этажа

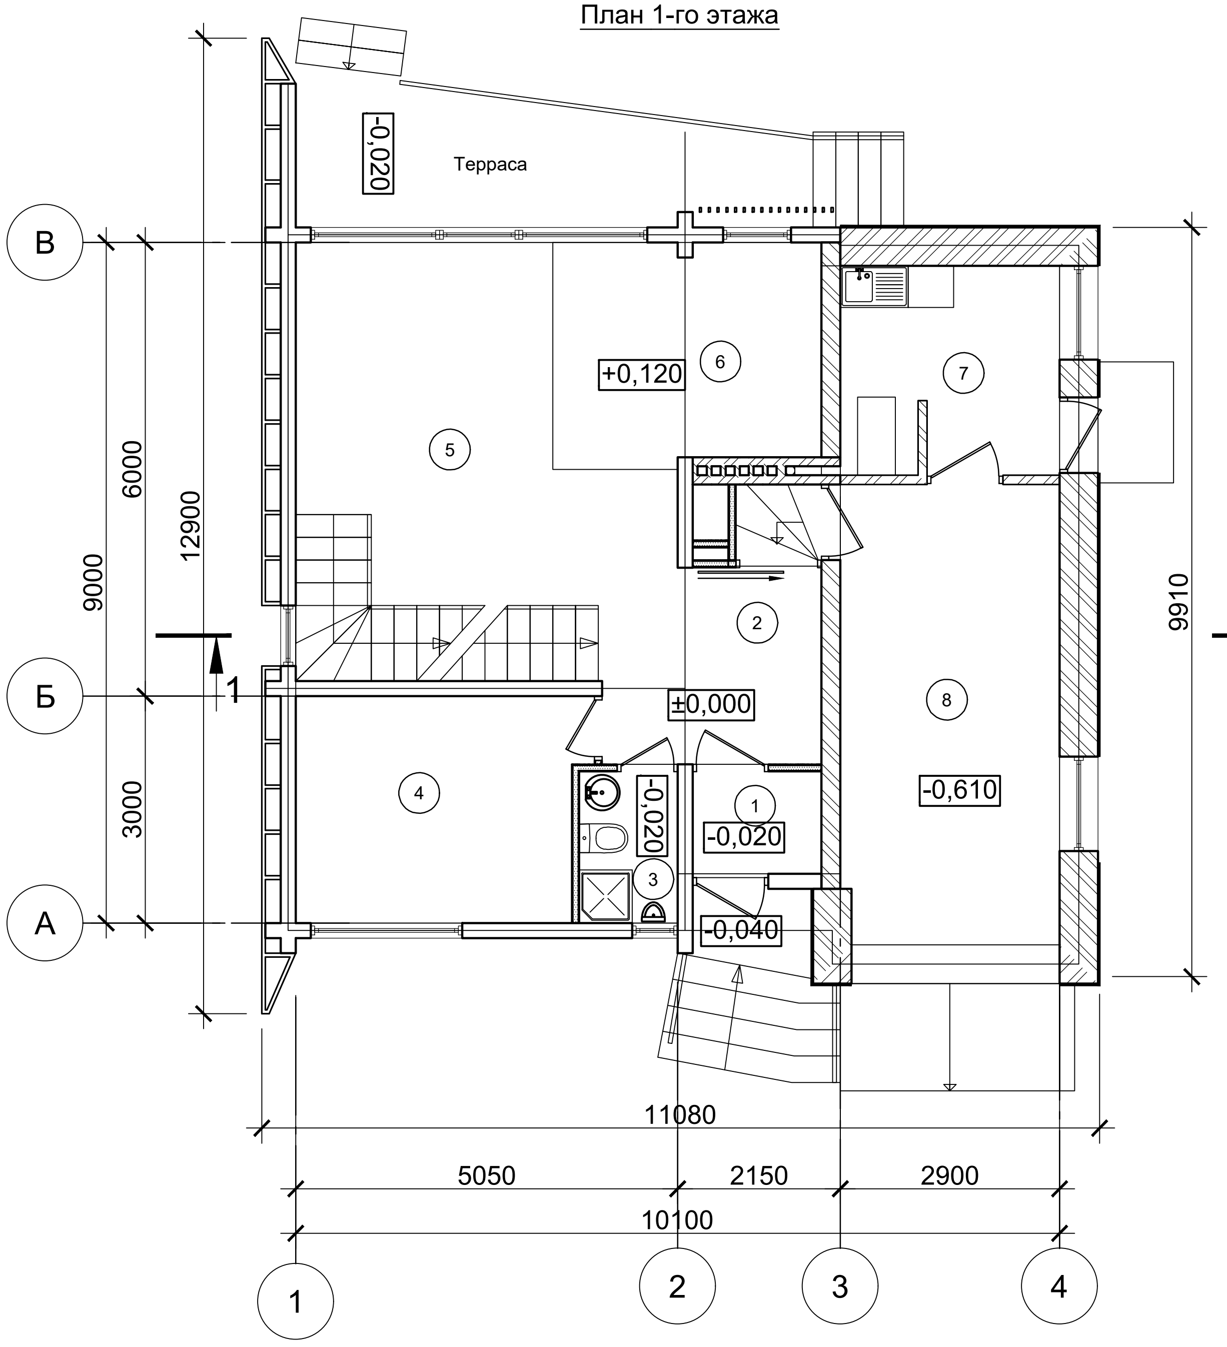

План мансардного этажа

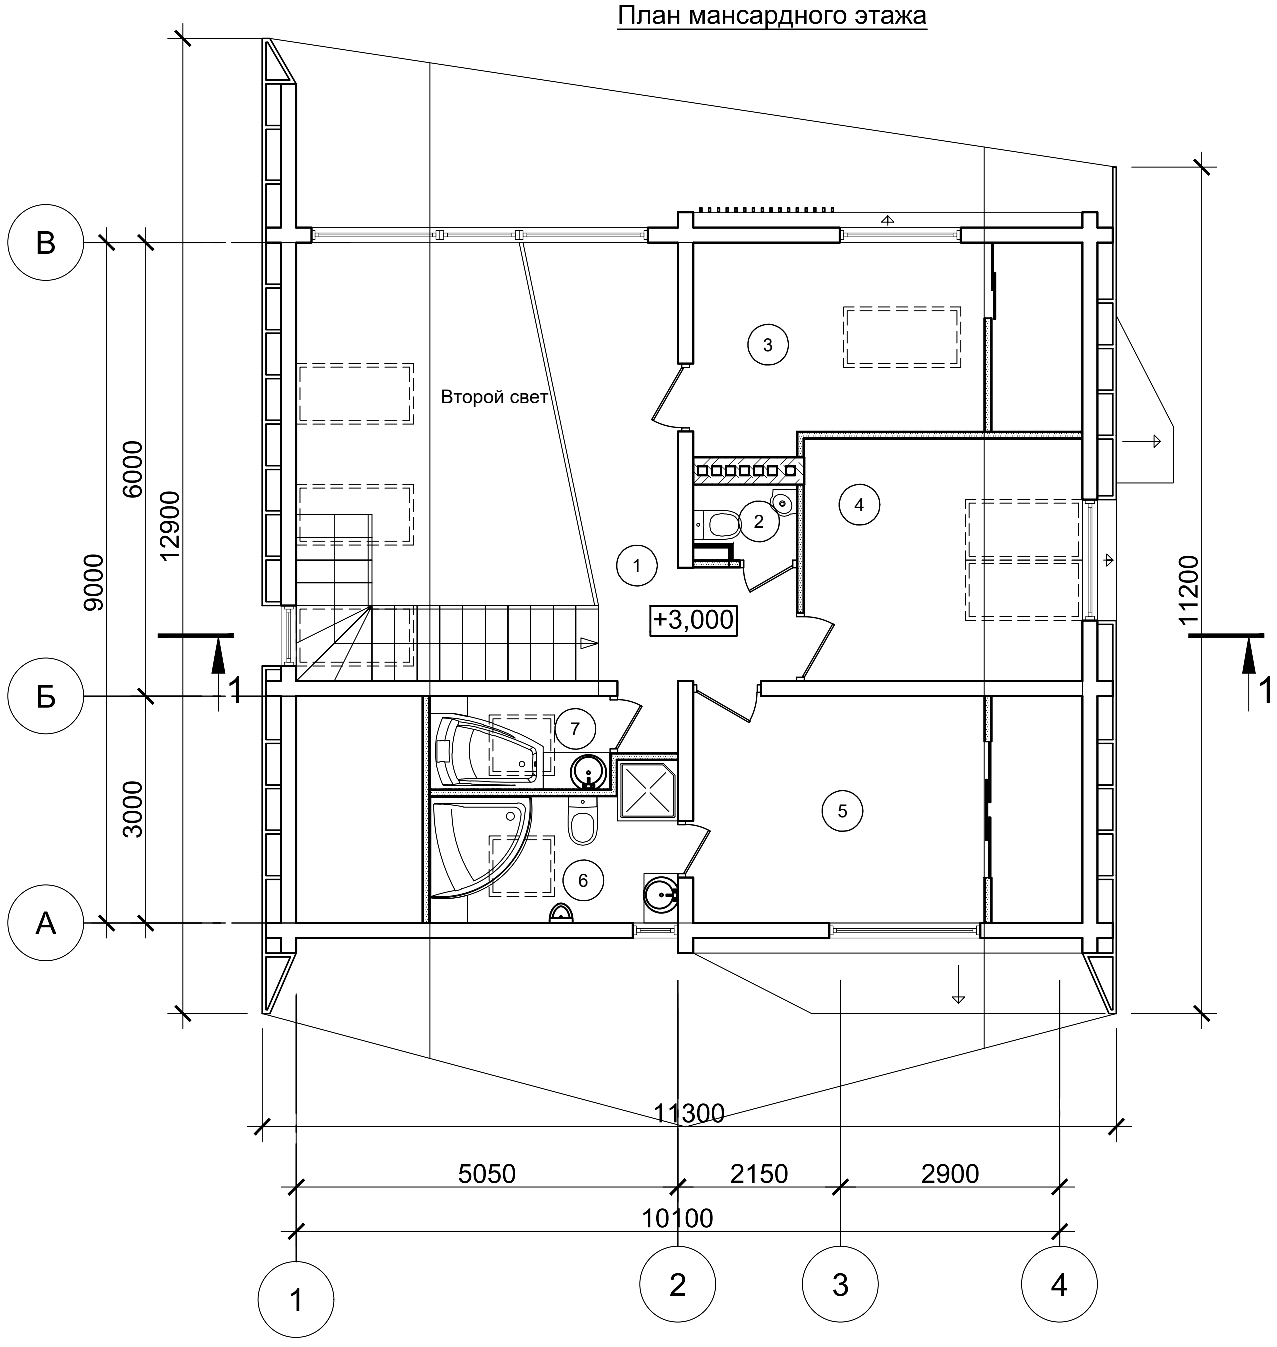

Экспликация помещений 1-го этажа

№ пом.	Наименование	Площадь м²	Кат. пом.
1	Тамбур	2,3	
2	Холл	7,3	
3	Санузел	2,6	
4	Спальня для гостей	11,2	
5	Гостиная	24,3	
6	Кухня-столовая	10,3	
7	Миникотельная	7,9	
8	Гараж	17,6	

Экспликация помещений мансардного этажа

№ пом.	Наименование	Площадь м²	Кат. пом.
1	Холл	11,6	
2	Туалет	1,3	
3	Спальня+гардеробная	13,3	
4	Спальня	11,8	
5	Спальня+гардеробная	15,5	
6	Санузел	5,9	
7	Ванная комната	2,9	

Взам. инв. №
Подп. и дата
Инв. № подл.

-АР

4

План 1-го этажа; План мансардного этажа.

Копировал
А3

План кровли

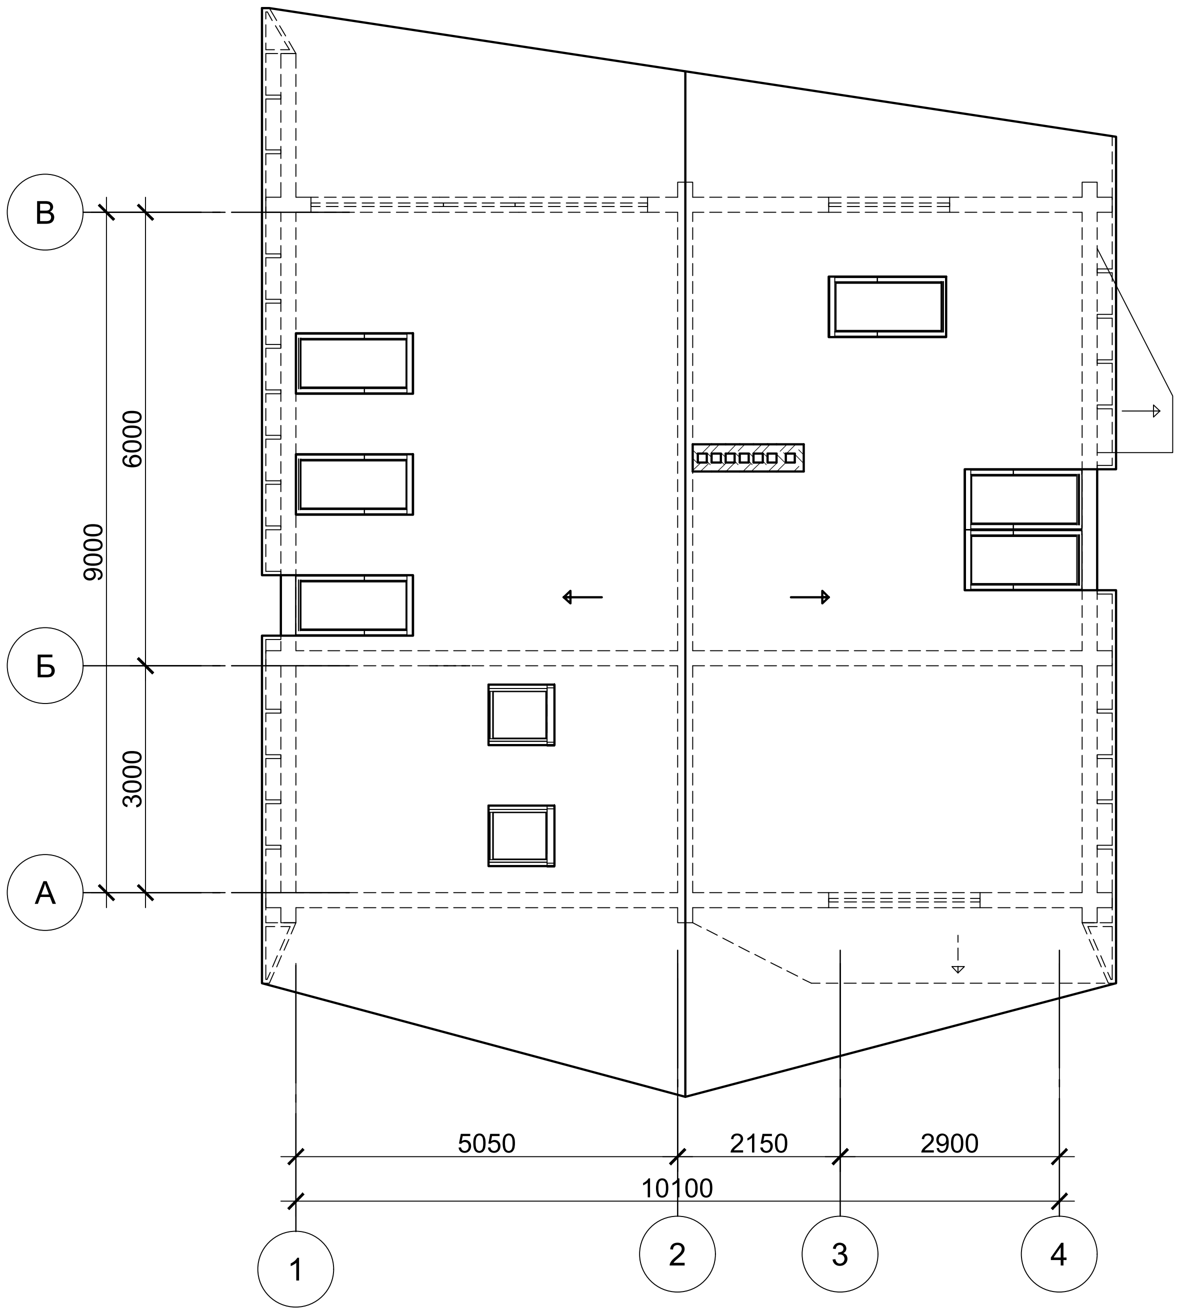

Разрез 1-1

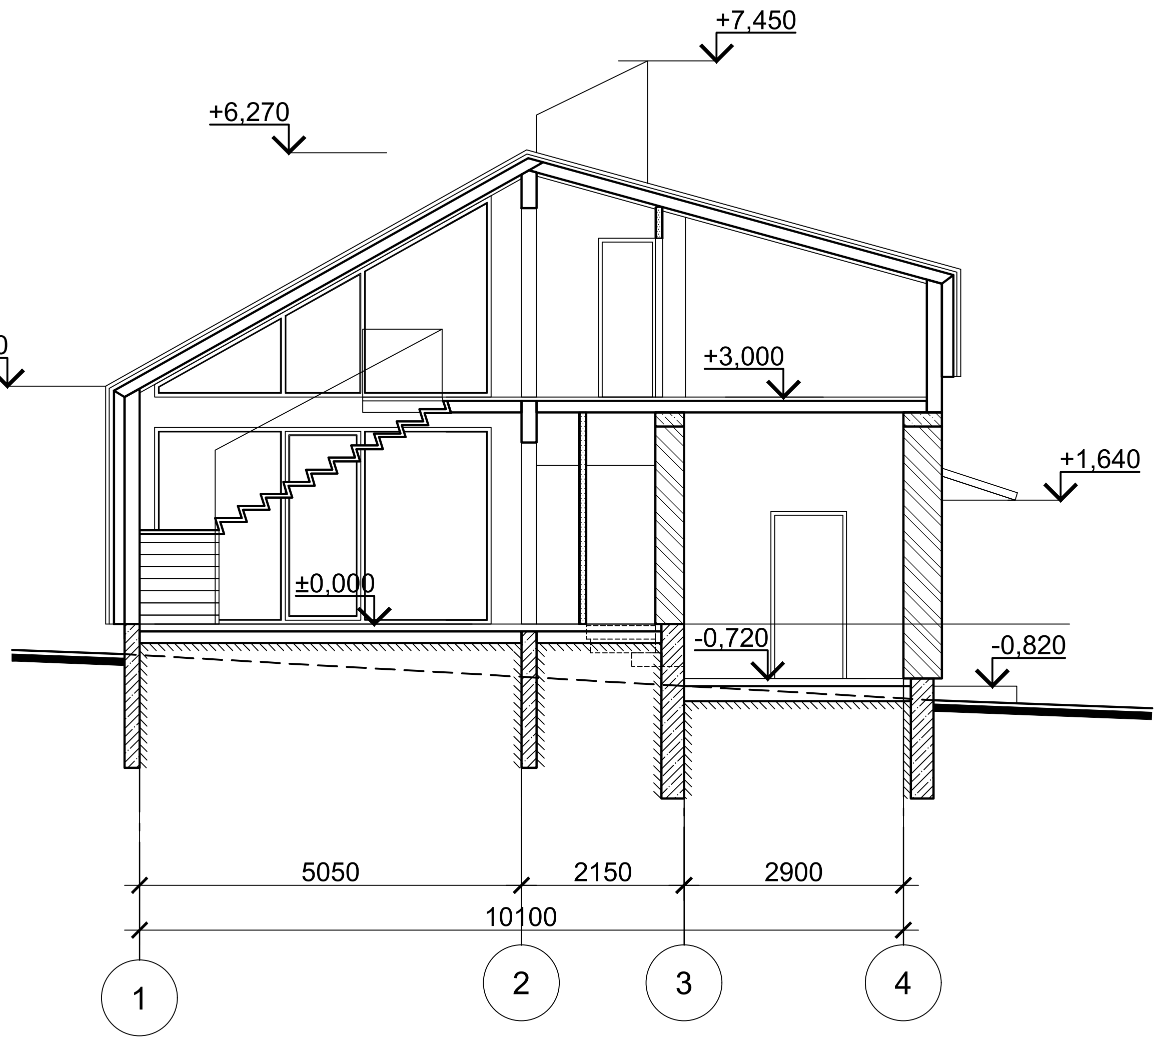

Взам. инв. №

Подп. и дата

Инв. № подл.

-АР

5

План кровли; Разрез 1-1.

Копировал

А3

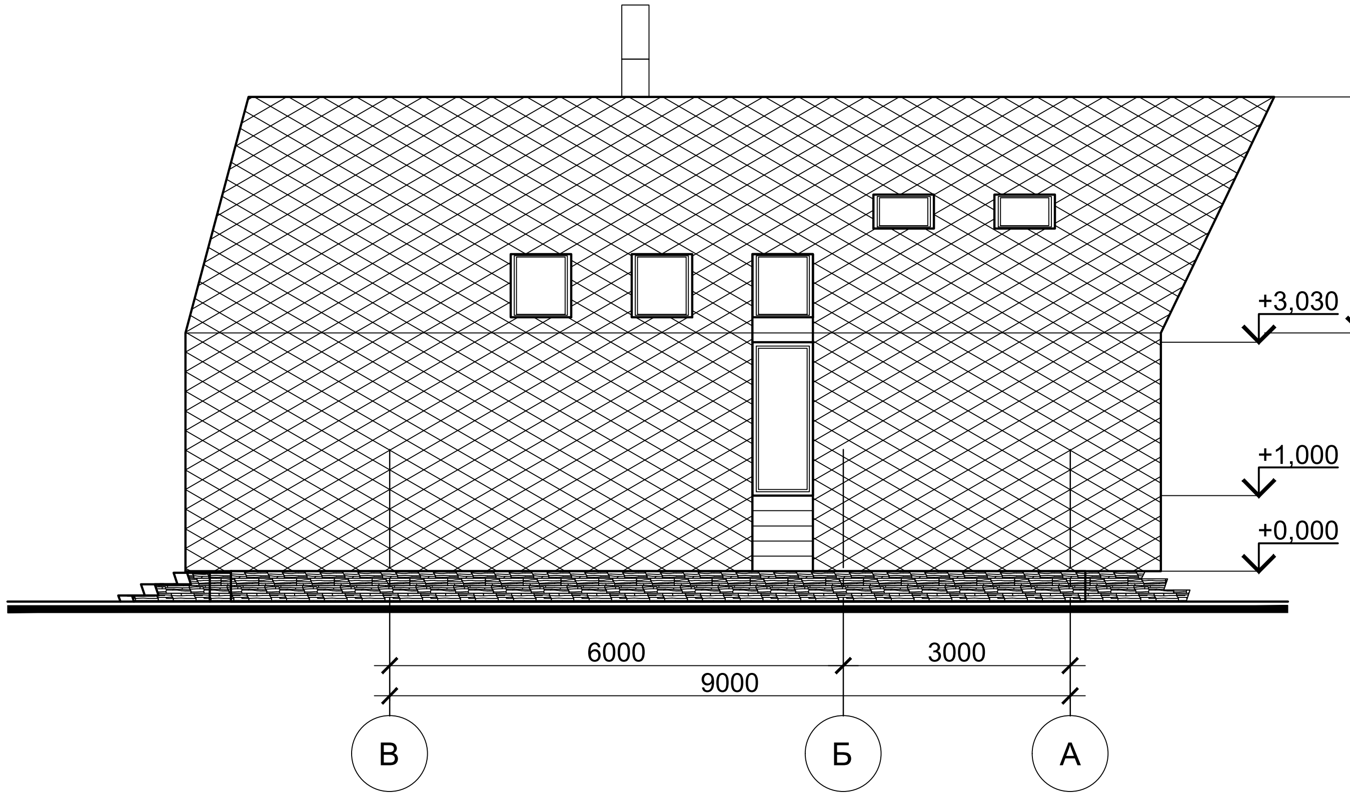

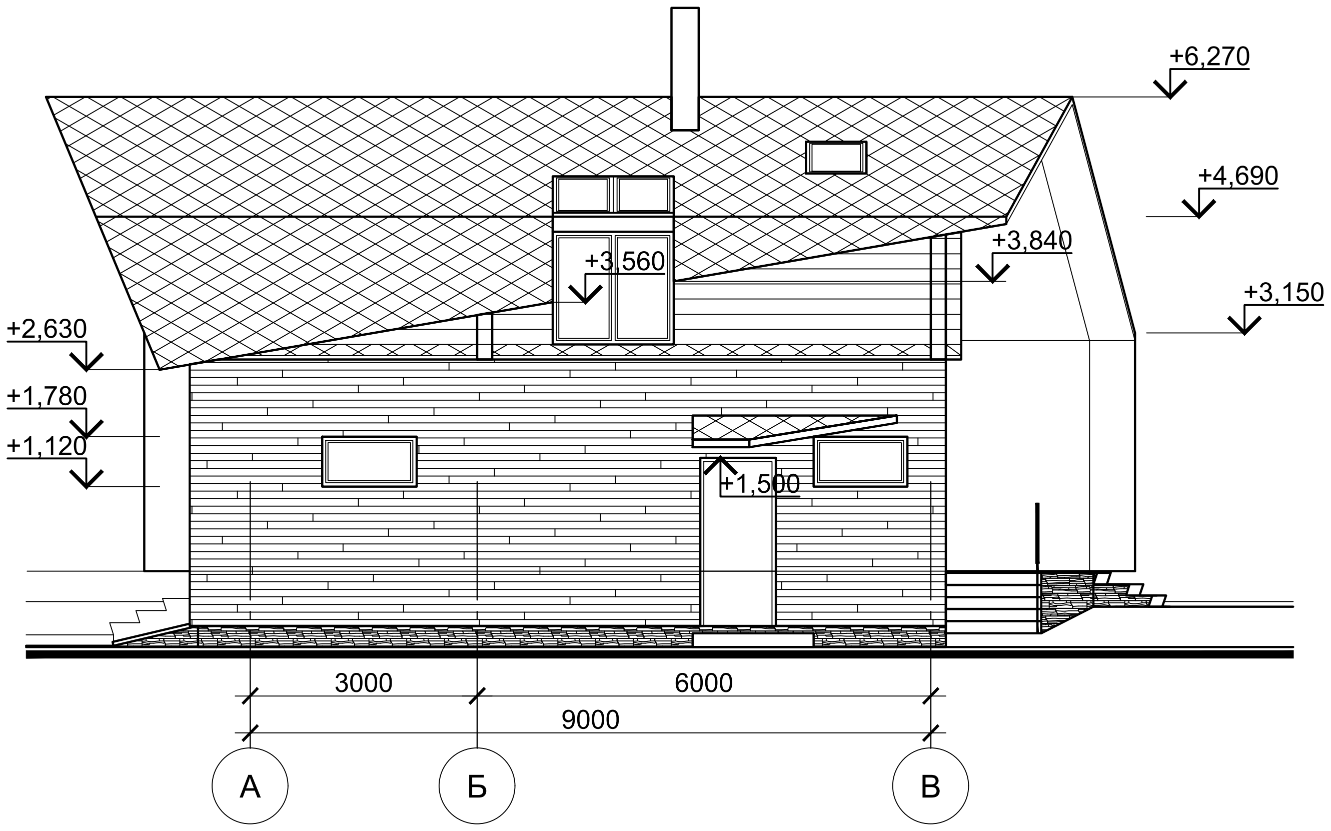

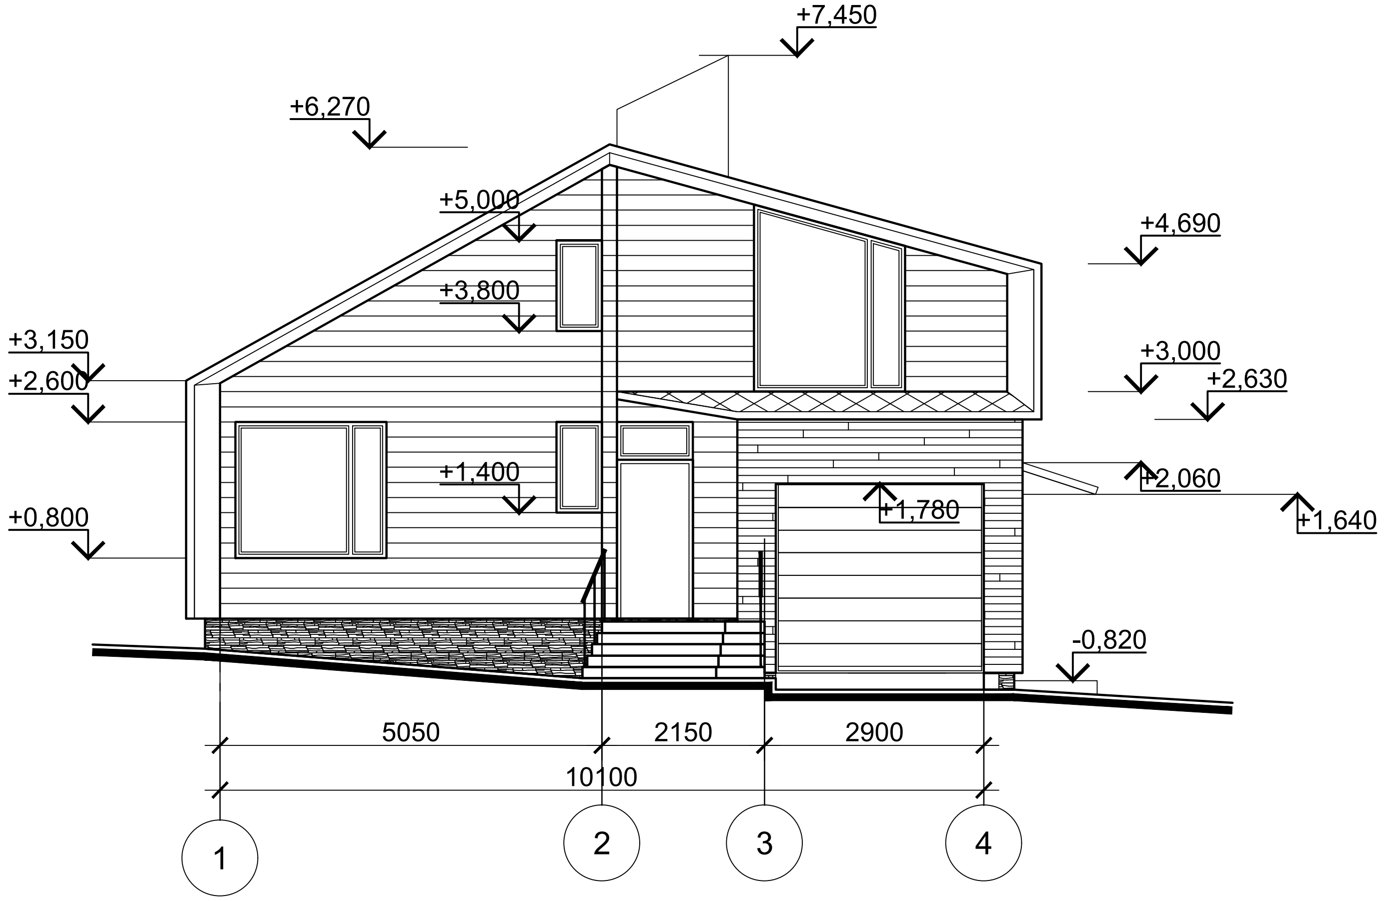

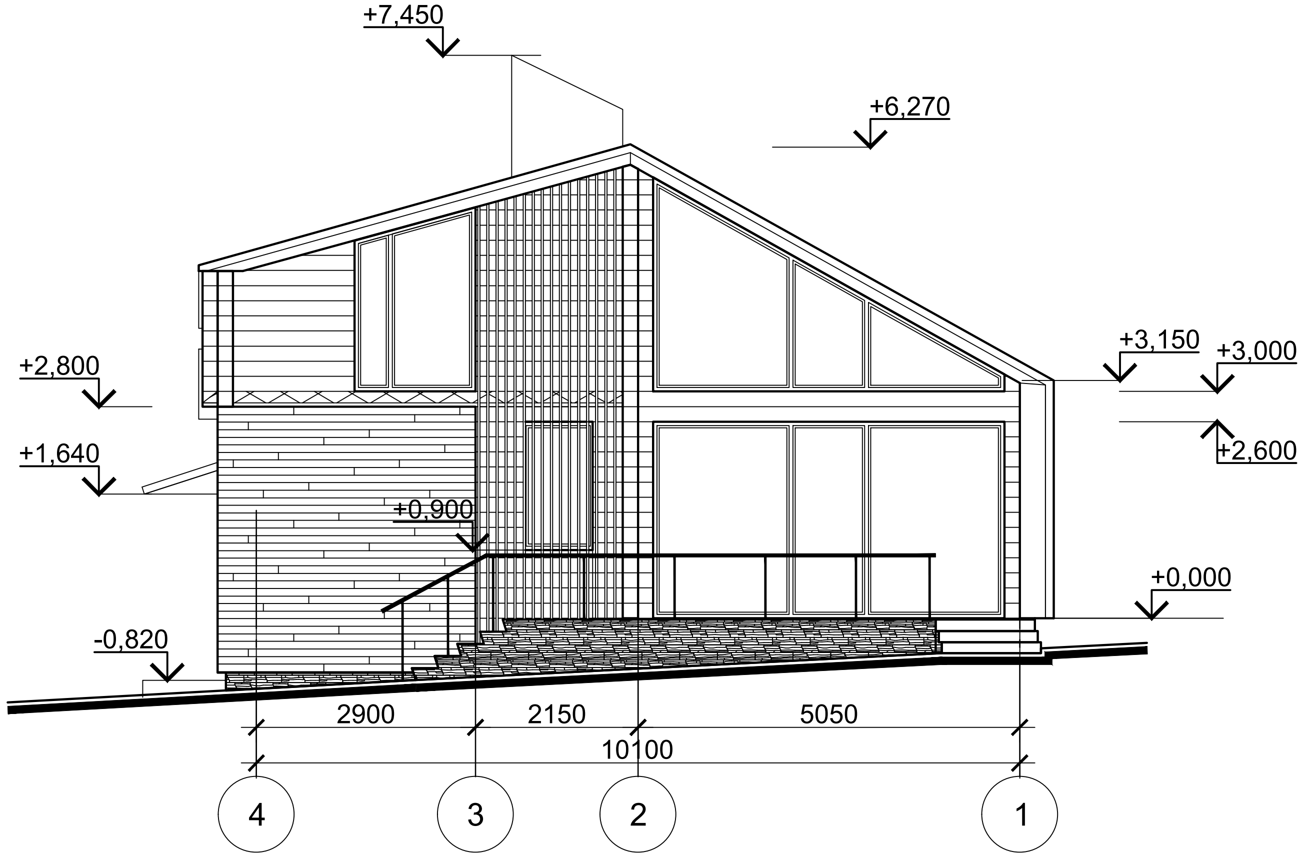

Взам. инв. №
Подп. и дата
Инв. № подл.

-АР

6

Фасады здания

План 1-го этажа

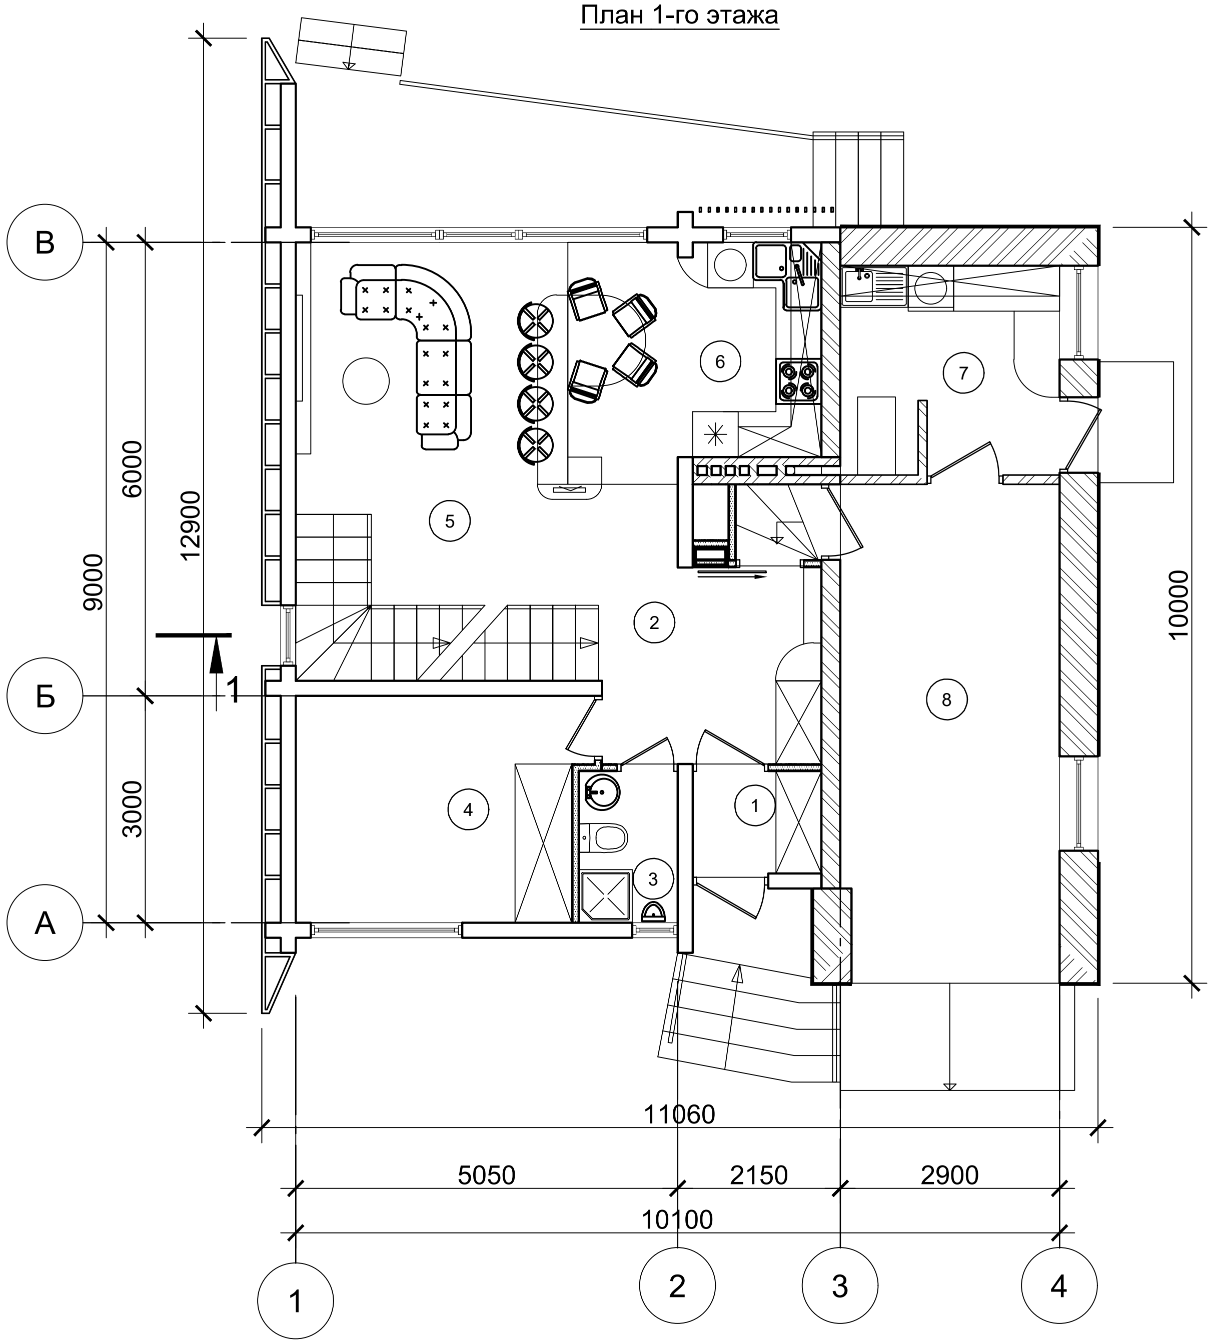

План мансардного этажа

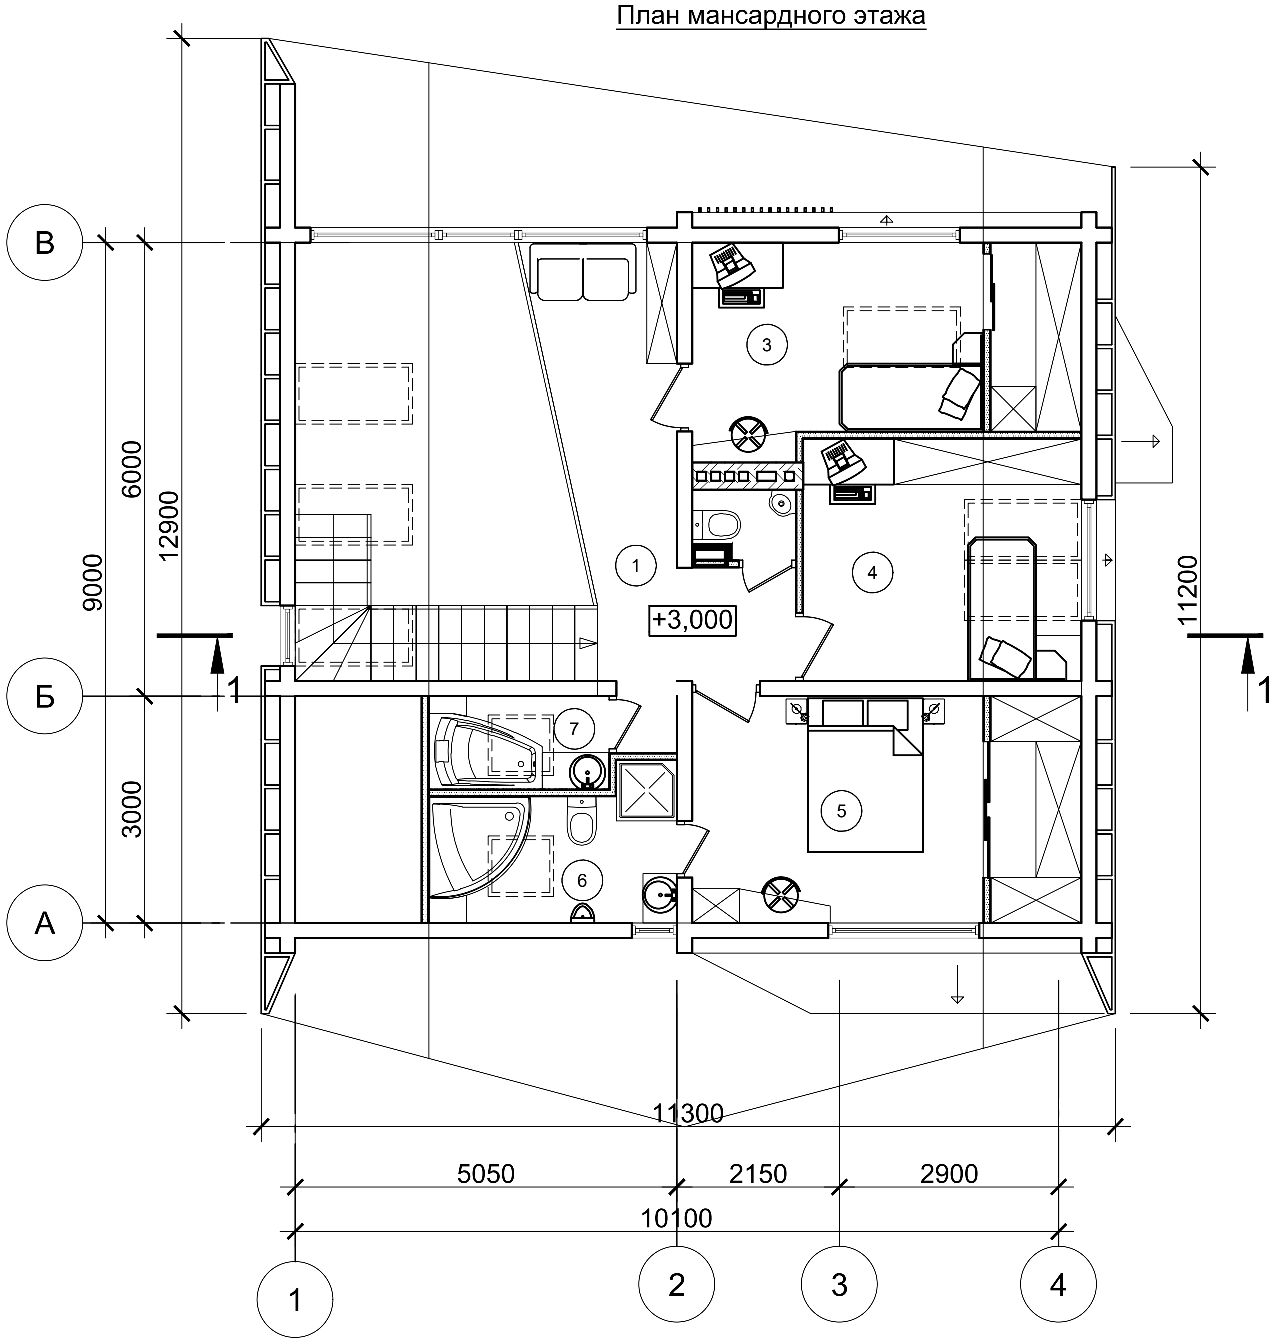

Экспликация помещений 1-го этажа

№ пом.	Наименование	Площадь м²	Кат. пом.
1	Тамбур	2,3	
2	Холл	7,3	
3	Санузел	2,6	
4	Спальня для гостей	11,2	
5	Гостиная	24,3	
6	Кухня-столовая	10,3	
7	Миникотельная	7,9	
8	Гараж	17,6	

Экспликация помещений мансардного этажа

№ пом.	Наименование	Площадь м²	Кат. пом.
1	Холл	11,6	
3	Спальня+гардеробная	13,3	
4	Спальня	11,8	
5	Спальня+гардеробная	15,5	
6	Санузел	5,9	
7	Ванная комната	2,9	

Взам. инв. №

Подп. и дата

Инв. № подл

-АР

7

План размещения мебели 1-го и мансардного этажа.

Копировал

А3